

全屋日式定制 · 方案设计交付册

方案设计交付版 · 沿用R3设计条件 · 尺寸单位mm · 待现场复尺及厂家深化

全屋日式定制

方案设计交付册

SCHEMATIC DESIGN / R4

玄关 · 客餐厅 · 厨房

主卧 · 次卧 · 卫浴

主阳台 · 生活阳台



项目	本次交付
文件用途	方案确认、定制询价及厂家深化输入
图纸组成	总说明 → 总平面 → 分空间 → 节点 → 清单 → 核验与版本
设计基线	R3模型与六册指引修订；保留用户风水、电器及固定床要求

图纸目录（一）

方案设计交付版 · 沿用R3设计条件 · 尺寸单位mm · 待现场复尺及厂家深化

图号	图纸名称	页码	比例口径
A-00	全屋日式定制 · 方案设计交付册	01	示意
A-01	图纸目录（一）	02	示意
A-02	图纸目录（二）	03	示意
A-03	设计总说明与交付边界	04	示意
A-04	设计风格与饰面意向	05	示意
P-01	参考建筑平面	06	1:50
P-02	全屋家具与定制柜布置平面	07	1:50
P-03	定制柜编号与分册索引	08	示意
E-01	玄关平面索引与空间示意	09	示意
E-02	玄关柜体正投影展开	10	示意
E-03	鞋包柜立面与分格	11	示意
E-04	入户隔视界面控制	12	示意
L-01	客餐厅平面索引与空间示意	13	示意
L-02	客餐厅柜体正投影展开	14	示意
L-03	电视墙立面定位	15	示意
L-04	餐厨服务带使用与设备控制	16	示意
K-01	厨房平面索引与空间示意	17	示意
K-02	厨房柜体正投影展开	18	示意
K-03	厨房台面与功能分段	19	示意
K-04	烟灶与凯度接口条件	20	示意
K-05	双槽联合湿区剖示	21	示意
M-01	主卧平面索引与空间示意	22	示意
M-02	主卧柜体正投影展开	23	示意
M-03	M2衣柜挂衣尺寸控制	24	示意
M-04	M3梳妆位与可关闭镜面	25	示意
M-05	床与飘窗高度关系	26	示意
S-01	次卧平面索引与空间示意	27	示意

目录条目和PDF书签均可点击跳转。R4为本册编排版本，三维几何仍以R3为设计基线。

图纸目录（二）

方案设计交付版 · 沿用R3设计条件 · 尺寸单位mm · 待现场复尺及厂家深化

图号	图纸名称	页码	比例口径
S-02	次卧柜体正投影展开	28	示意
S-03	S2衣柜分格尺寸控制	29	示意
S-04	S3窗下柜与空调避让	30	示意
B-01	卫浴平面索引与空间示意	31	示意
B-02	卫浴柜体正投影展开	32	示意
B-03	卫浴净空与淋浴入口控制	33	示意
B-04	盆柜与镜柜分格控制	34	示意
U-01	阳台与生活阳台平面索引与空间示意	35	示意
U-02	阳台与生活阳台柜体正投影展开	36	示意
U-03	家政柜与洗衣台控制	37	示意
U-04	生活阳台低柜与设备维护	38	示意
D-01	柜体通用构造与厂家深化节点	39	示意
D-02	灯光与设备接口功能要求	40	示意
T-01	柜体与保留家具总表（一）	41	示意
T-02	柜体与保留家具总表（二）	42	示意
T-03	饰面与基材选型表	43	示意
T-04	五金配置与验收表	44	示意
T-05	电器及设备条件表（一）	45	示意
T-06	电器及设备条件表（二）	46	示意
Q-01	风水要求落实与待核事项	47	示意
Q-02	复尺、选型及生产前确认清单	48	示意
R-01	设计依据与版本说明	49	示意
R-02	修订记录与交付范围	50	示意

目录条目和PDF书签均可点击跳转。R4为本册编排版本，三维几何仍以R3为设计基线。


设计总说明与交付边界

方案设计交付版 · 沿用R3设计条件 · 尺寸单位mm · 待现场复尺及厂家深化

条款	设计说明
01 资料依据	7楼同户型参考模型、用户要求、六册精细化指引及已提供的设备安装资料；不是20楼现场测绘。
02 图纸顺序	A设计说明；P总平面；E/L/K/M/S/B/U分空间；D节点功能；T清单；Q确认；R来源与版本。
03 编号原则	沿用3D对象编号，例如R1鞋柜、L2电视低柜、M1/S1床；图号E-03不是柜号。表单补列不代表新增柜体。
04 尺寸原则	默认mm。外包宽深高、设备安装净孔、完成面标高、活动使用净空分开。冲突处先复尺，不按比例反量下单。
05 图示状态	实线为可见构件/外包；虚线为高位投影或条件参考。正投影可能省略衣物、门板或背板，详见页内说明。
06 方案不变项	双固定床、实墙床头、可关闭镜、双槽、750×600冰箱控制体量、米家烟灶、独立微波和凯度需求保留。
07 条件项	灶下凯度叠放、真实门位、床窗完成面、外窗安全、设备维护与环境适用必须确认，不以渲染代替认可。
08 交付边界	可用于方案讨论和定制询价；不含结构改造、电气回路/线径、给排水施工坐标、厂家拆单、责任签章。

设计风格与饰面意向

方案设计交付版 · 沿用R3设计条件 · 尺寸单位mm · 待现场复尺及厂家深化

 

暖白平板

主门板 / 可握把手



浅木色

内格 / 局部台面



耐湿细部

封边孔口 / 可换五金

颜色看实体样板；报价写材料、批次、五金型号及售后，不能只写“日式”。

干区柜

18板厚是当前几何占位，板材/背板构造另定；长层板、2700高门分扇、挂杆和吊柜固定按荷载核。内格排孔可调，开孔封口完整；材料检测与批次、封边及售后写进报价。

湿区与阳台

水槽柜、浴室柜、阳台分开选材和防腐五金；可取托盘不能替代建筑防水。易湿接缝、穿板管孔和柜脚做好隔水细部；高柜固定在能承载的实体界面，不锚在栏杆或窗框。


控制维护复杂度

不为日式外观把全屋改成反弹器、复杂旋转篮、无法拆洗的细格栅。主卧折门确因窄通道需要，须做成套五金样板；滑轨、铰链、灯具驱动写型号，可单件替换。

依据 | G02 p127-138；G03 p82-96；G04 p14、44；G05环境与维护方法

参考建筑平面

方案设计交付版 · 沿用R3设计条件 · 尺寸单位mm · 待现场复尺及厂家深化

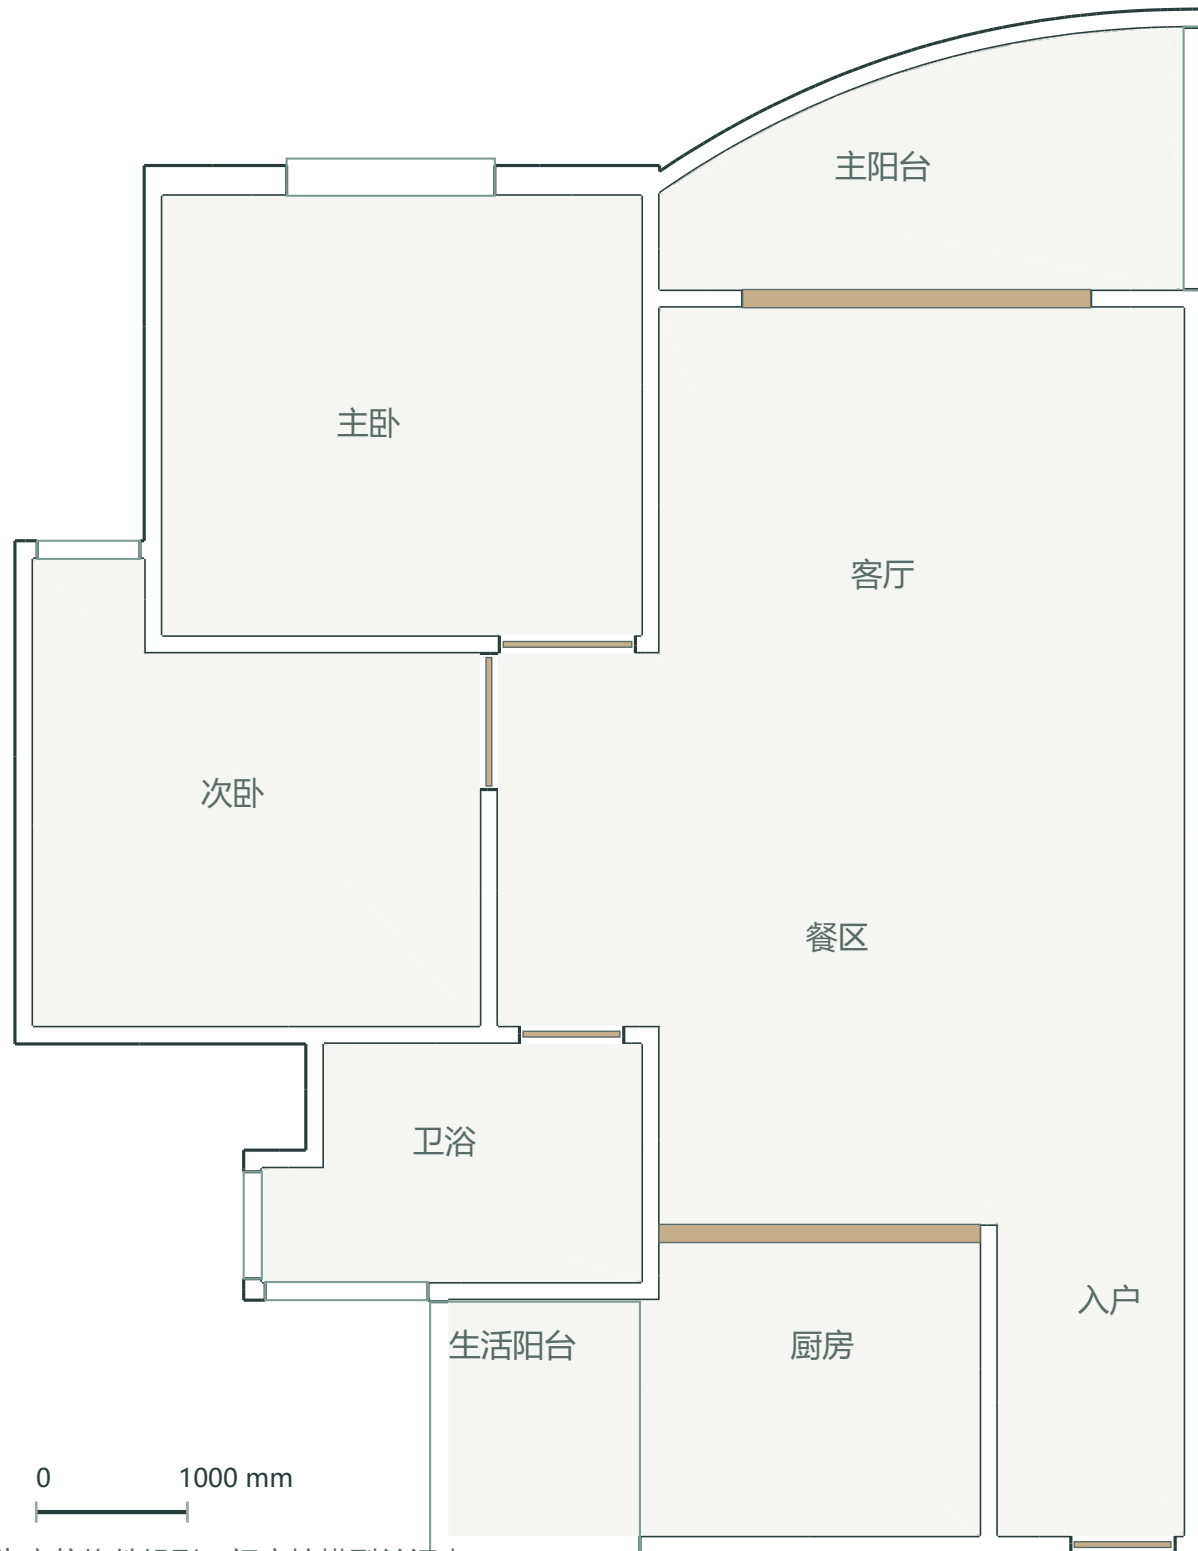

水平剖切约1200；虚线为高位构件投影；门扇按模型关闭态。

图纸用途

参考建筑平面显示模型墙窗和门位；布置平面叠加家具、定制柜及编号。无新增拆墙或移门指令。

比例与测量

A3原尺寸打印时1:50。只取标注值；模型三角面和门窗轮廓并非现场竣工测量。

门位优先复核


二维资料与模型的卧室、卫浴、厨房门位存在冲突。此图保留模型，未宣称现场门冲已消除。

方向口径

延用用户资料：图上约西北、图下约东南；未测罗盘角度，不画精确方位宫界。

全屋家具与定制柜布置平面

方案设计交付版 · 沿用R3设计条件 · 尺寸单位mm · 待现场复尺及厂家深化

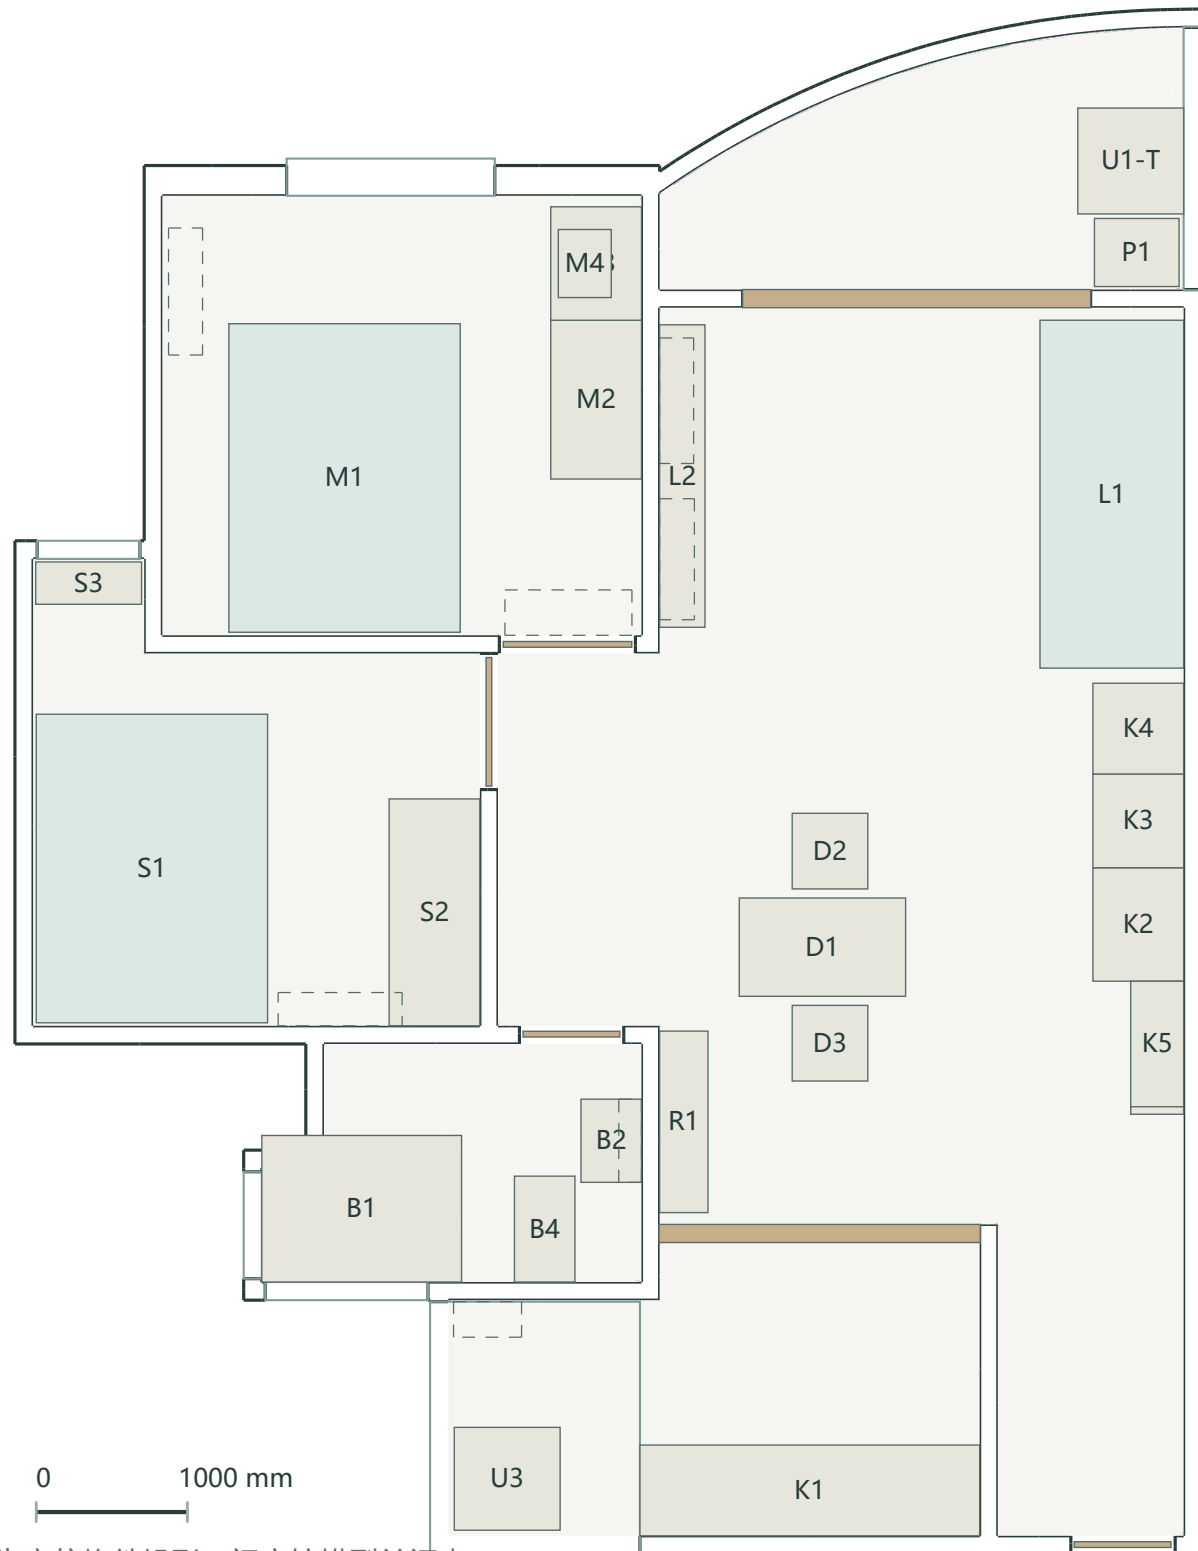

水平剖切约1200；虚线为高位构件投影；门扇按模型关闭态。

图纸用途

参考建筑平面显示模型墙窗和门位；布置平面叠加家具、定制柜及编号。无新增拆墙或移门指令。

比例与测量

A3原尺寸打印时1:50。只取标注值；模型三角面和门窗轮廓并非现场竣工测量。

门位优先复核

二维资料与模型的卧室、卫浴、厨房门位存在冲突。此图保留模型，未宣称现场门冲已消除。

方向口径

延用用户资料：图上约西北、图下约东南；未测罗盘角度，不画精确方位宫界。

定制柜编号与分册索引

方案设计交付版 · 沿用R3设计条件 · 尺寸单位mm · 待现场复尺及厂家深化


空间	主要对象编号	首图	索引说明
玄关	R1	E-01	入口不加横屏风，柜体沿卫生间外侧实墙；换鞋椅用后归位。门位及弱电箱现场确认。
客餐厅	L2 / L2-U / K5 / K3 / K4	L-01	沙发实墙背靠，保留2300×950紧凑四人直排；餐桌1100×650。设备开门与餐椅拉出分时。
厨房	K1	K-01	固定2247宽链；双槽、600洗碗机、米家烟灶保留。凯度灶下为条件方案，不是已批准安装。
主卧	M2 / M3 / M5	M-01	保留1500×2000床垫和实体床头；关闭态柜前599、床侧440为参考窄点。镜可关闭，床头无深重吊柜。
次卧	S2 / S3	S-01	保留固定1500×2000床；柜前804、床尾进入窄点402，不表述为舒适通道。保留空调检修退台。
卫浴	B2 / B3	B-01	保持原排污和浅盆方案，门位冲突须先复尺；盆前凸量、淋浴入口及门扇扫掠单独核。
阳台与生活阳台	P1 / U1-T / U3	U-01	主阳台端部洗衣、家政，中央留采光与晾晒；生活阳台U3为低柜，不密闭包裹燃气设备。

K2冰箱为设备控制区；M1/S1为保留床；3D里R1即鞋包柜，不再使用另一套E1别名。完整对象见T-01/T-02。


玄关平面索引与空间示意

方案设计交付版 · 沿用R3设计条件 · 尺寸单位mm · 待现场复尺及厂家深化

01 / 空间平面与柜号

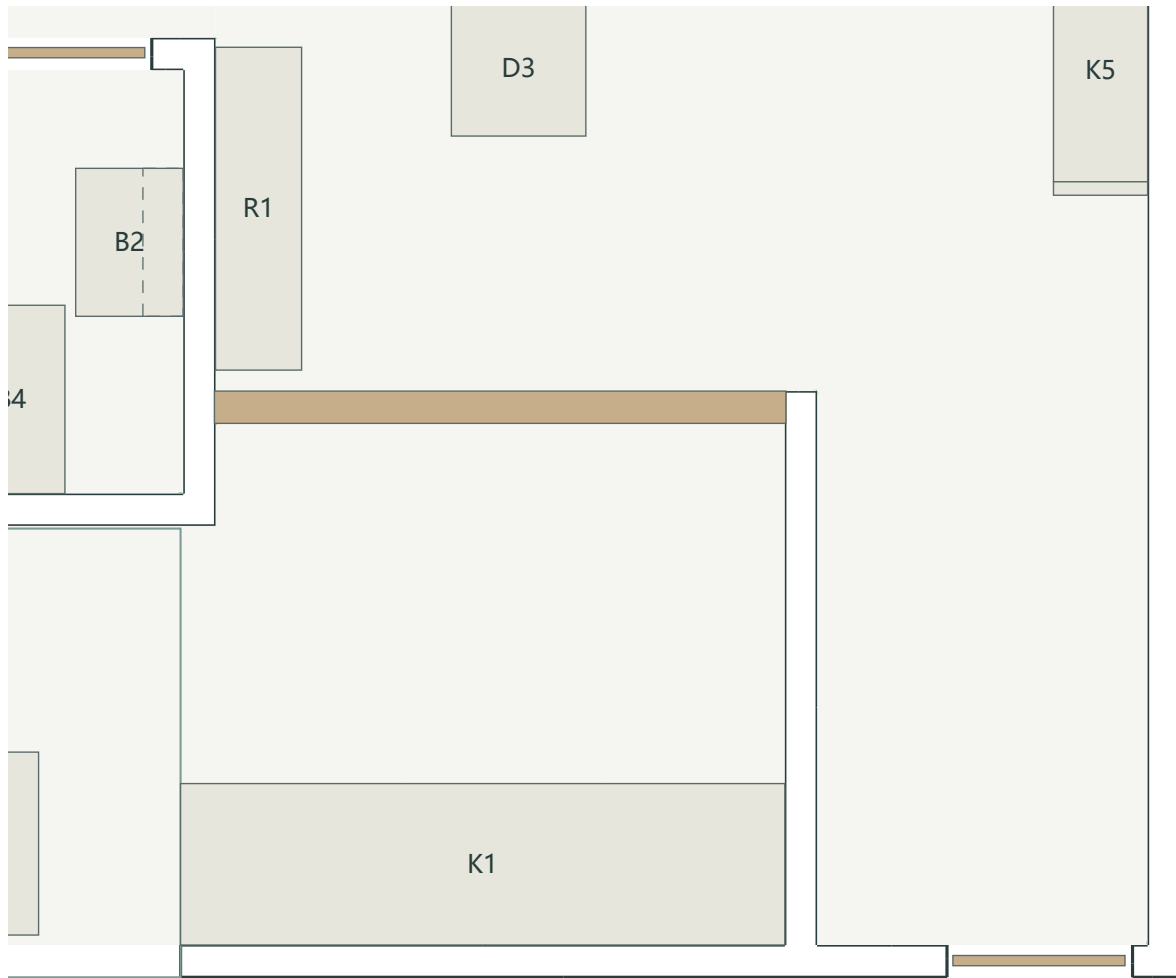

02 / 关闭外观

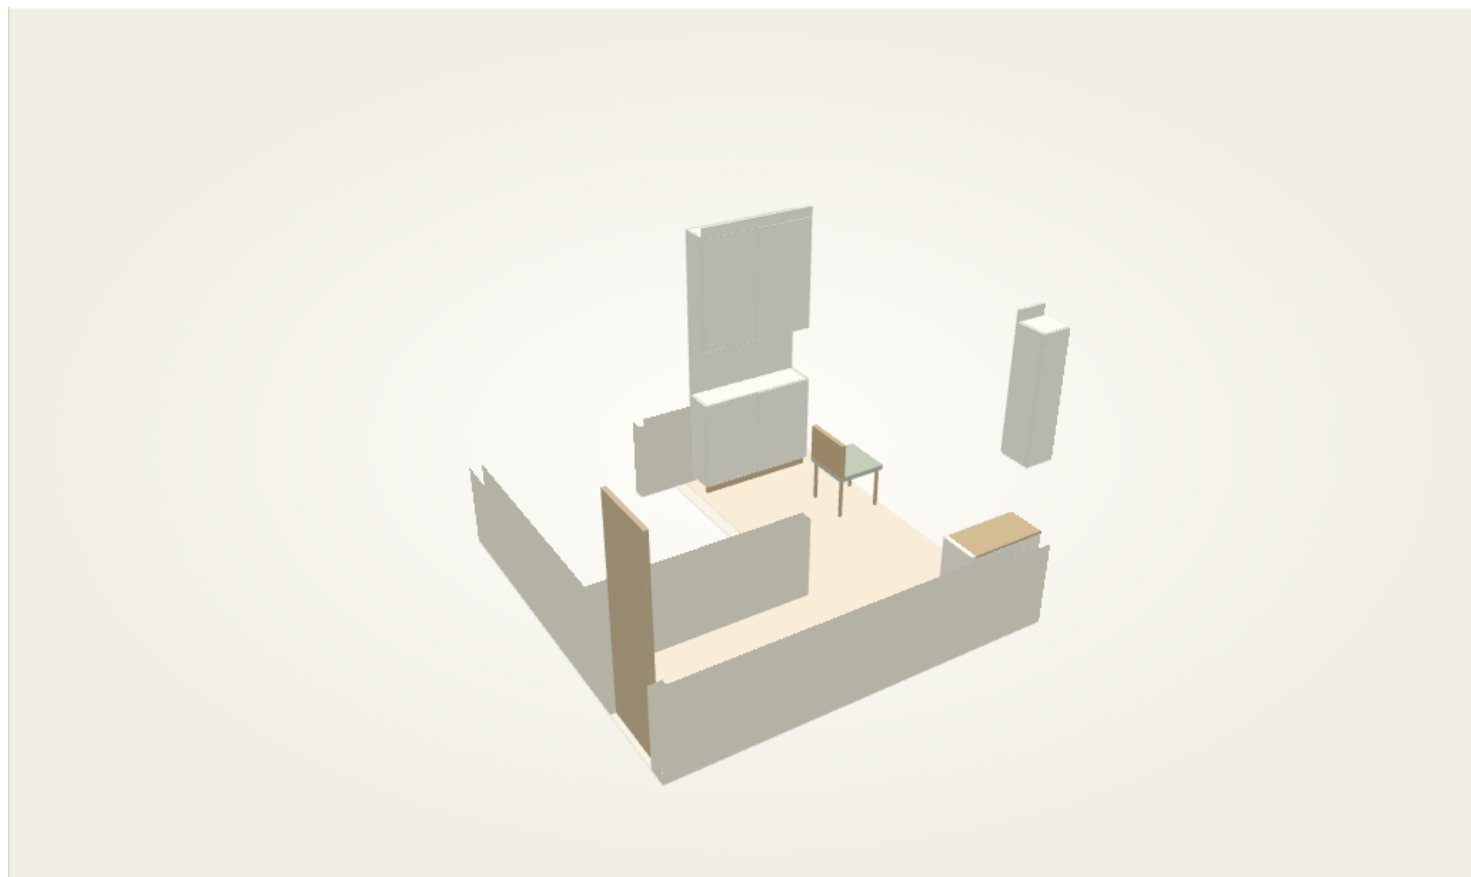

布置与使用要求

入口不加横屏风，柜体沿卫生间外侧实墙；换鞋椅用后归位。门位及弱电箱现场确认。


读图及现场确认

平面编号与P-03、T-01/T-02对应；正立面按柜体朝向展开。三维图为剖墙示意，不是照片级效果图。尺寸和设备以本册控制值及复尺结果联合确认。


玄关柜体正投影展开

方案设计交付版 · 沿用R3设计条件 · 尺寸单位mm · 待现场复尺及厂家深化


R1 / 正立面

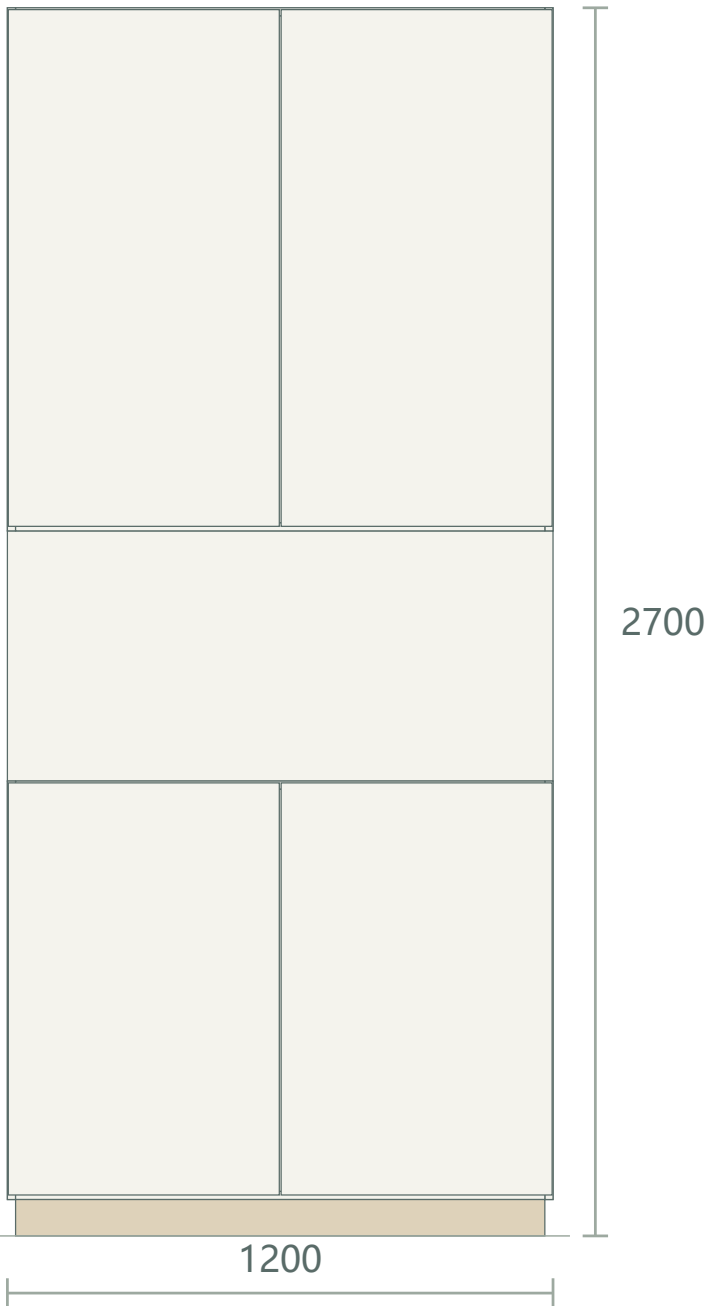

R1 / 去门板内部投影

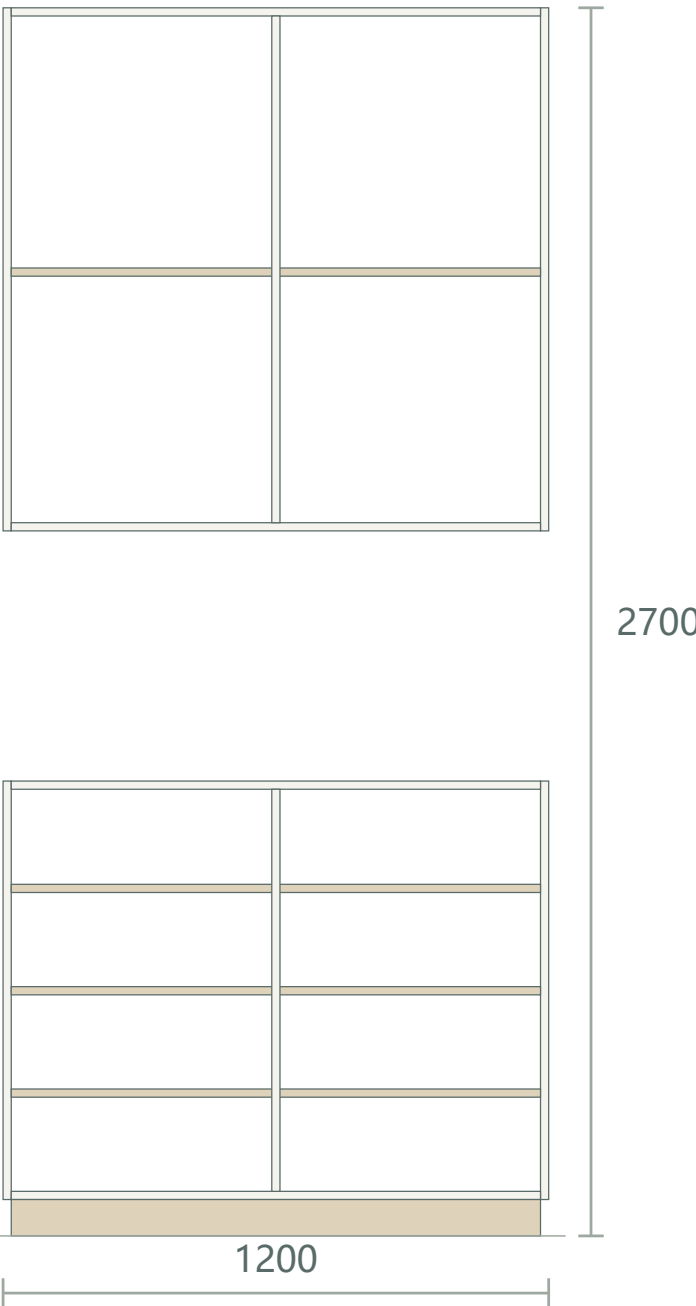


R1 / 侧向内部投影

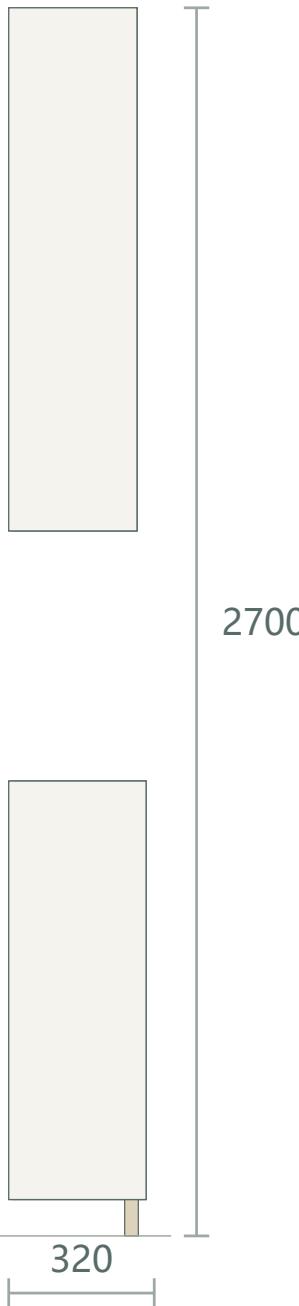

沿模型轴递增展开，非站位左右。侧向是内部投影，非施工剖切节点。标注柜体外包尺寸；内部去除门板和背板，非取消构件。

鞋包柜立面与分格

方案设计交付版 · 沿用R3设计条件 · 尺寸单位mm · 待现场复尺及厂家深化

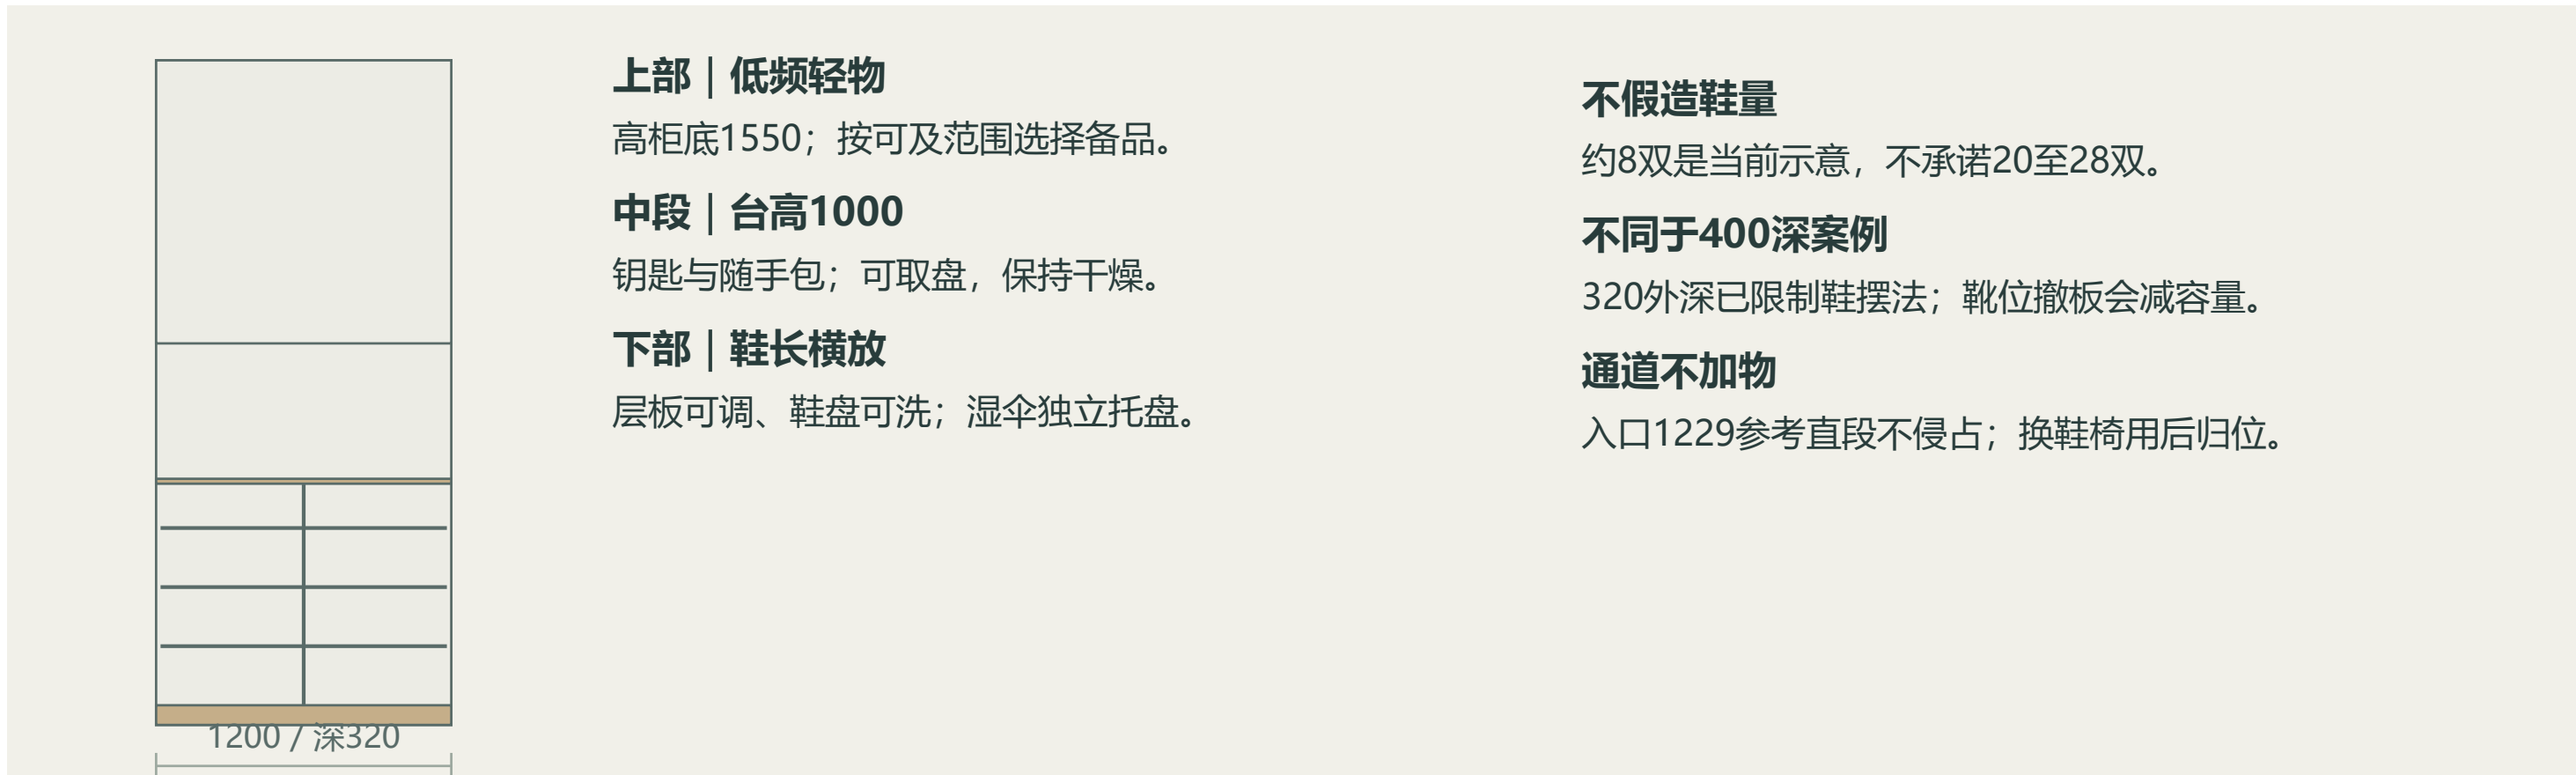

上部 | 低频轻物

高柜底1550；按可及范围选择备品。

中段 | 台高1000

钥匙与随手包；可取盘，保持干燥。

下部 | 鞋长横放

层板可调、鞋盘可洗；湿伞独立托盘。

不假造鞋量

约8双是当前示意，不承诺20至28双。

不同于400深案例

320外深已限制鞋摆法；靴位撤板会减容量。

通道不加物

入口1229参考直段不侵占；换鞋椅用后归位。

鞋柜内部分配

保留鞋长沿柜宽方向的横放逻辑；现模型约8双只是示意。先量最长鞋、靴筒和常穿双数，再用活动层板、可抽洗鞋盘调整。靴位撤一块层板取得连续净高，容量随之减少，不套400深鞋柜的双数。

湿物与落物台分开

中段台高1000，钥匙和随手包集中；柜内干鞋、湿伞/雨具分别设可取托盘，湿鞋先通风干燥再入柜。通风孔不被背板或靠墙封死，不把杀菌/烘鞋电器作为默认配置。

换鞋和弱电

用已有可移动餐椅临时换鞋后归位，不在窄点常放换鞋凳。弱电箱、配电箱待现场定位：留独立干燥检修区和门开启，不与湿鞋共仓，不假设已经藏进这只柜。

依据 | G04 p5、8-14、19、35、44、52-54、95-99

入户隔视界面控制

方案设计交付版 · 沿用R3设计条件 · 尺寸单位mm · 待现场复尺及厂家深化

入户开门

无横屏风；柜体沿侧边。

餐客厅

低柜与错位不等于挡住站立视线。

阳台界面

开：见景。
闭：透光不透视，需昼夜试样。

这是可切换的隐私方案，不是“永久通透又永久隔视”。

常态开敞

入口不设横屏风，高冰箱退到服务带；830×350餐边下柜不加深，400宽上柜保持退让。保留视线和转角，但如实标注打开阳台界面时仍可斜看远景。

需要严格隔视时

在既有阳台门室内侧配可闭合、透光不透视的分区遮蔽，白天近楼侧可单独遮，来客开门时可闭合。材料须在白天/夜晚两种背光条件试样；关闭会遮景，开启不保证隔视。轨道和门扇不能冲突。

保留的风水取舍


用真实可闭的界面满足隐私偏好，不以占通道屏风或摆件替代。不承诺同时完全通透、完全看不到阳台；公共走廊不放柜、不摆阵。

依据 | G04 p5；用户风水要求的入户开敞与隔视取舍


客餐厅平面索引与空间示意

方案设计交付版 · 沿用R3设计条件 · 尺寸单位mm · 待现场复尺及厂家深化

01 / 空间平面与柜号

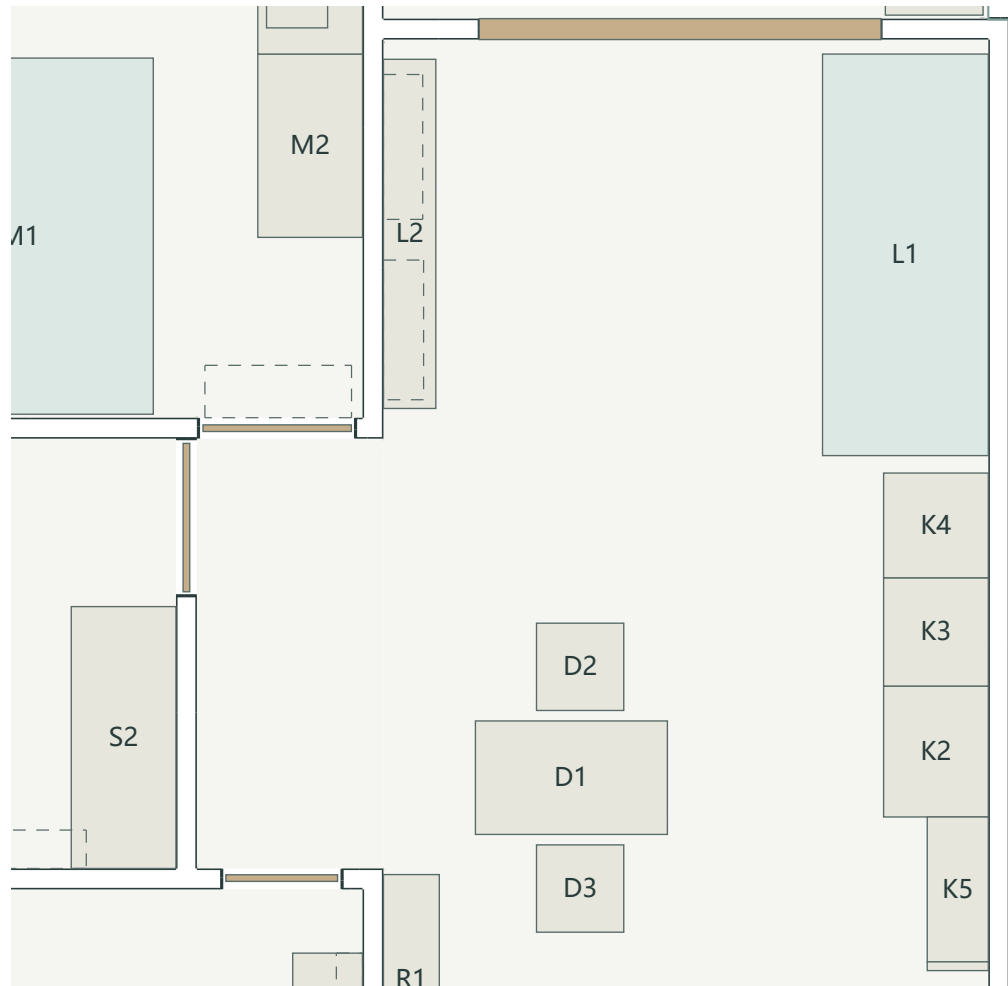

02 / 关闭外观

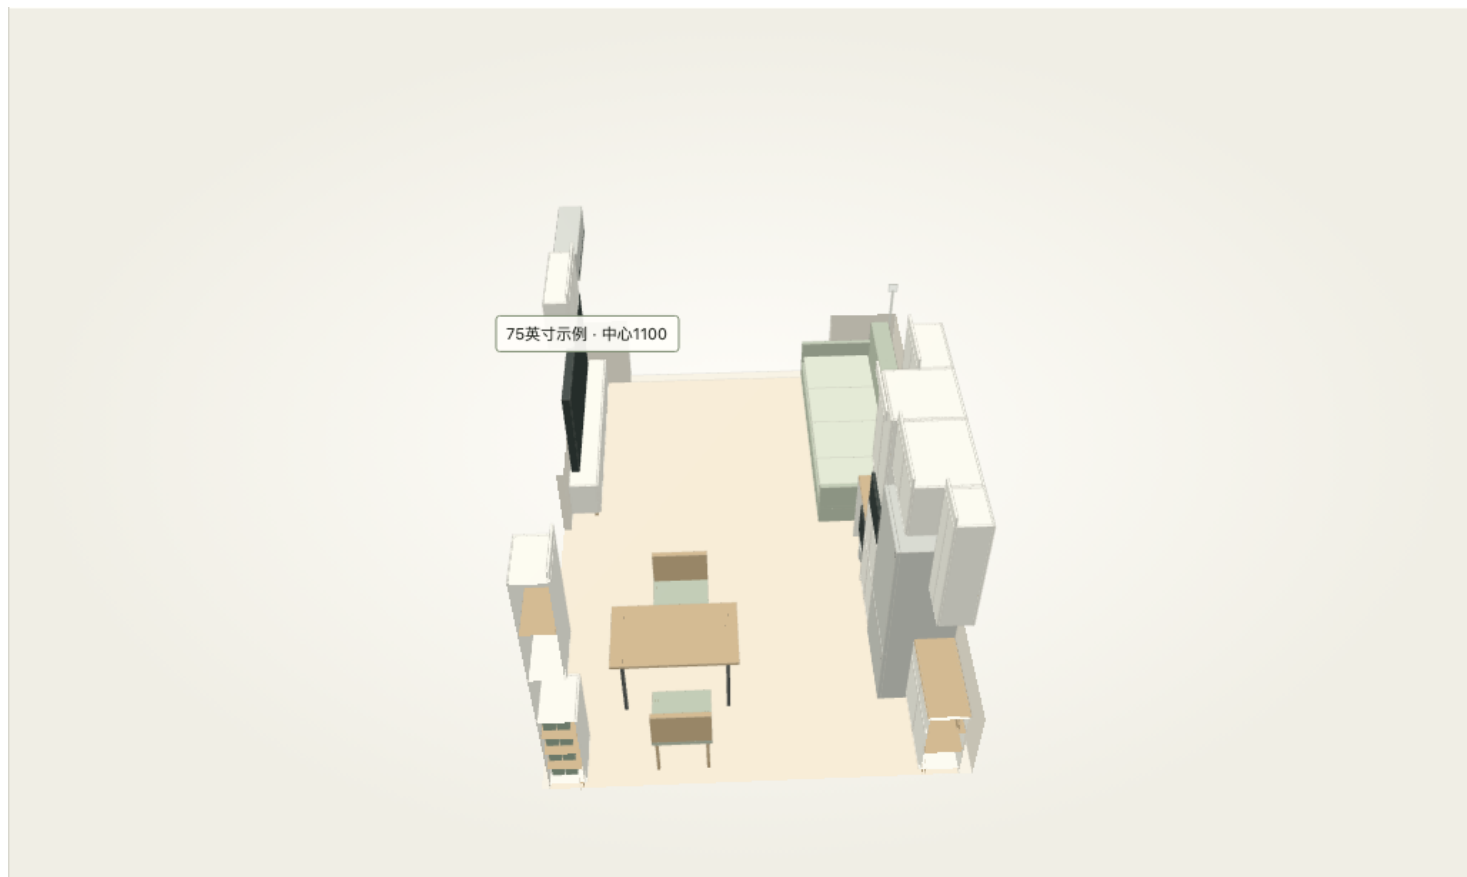

布置与使用要求

沙发实墙背靠，保留2300×950紧凑四人直排；餐桌1100×650。设备开门与餐椅拉出分时。


读图及现场确认

平面编号与P-03、T-01/T-02对应；正立面按柜体朝向展开。三维图为剖墙示意，不是照片级效果图。尺寸和设备以本册控制值及复尺结果联合确认。

客餐厅柜体正投影展开

方案设计交付版 · 沿用R3设计条件 · 尺寸单位mm · 待现场复尺及厂家深化


L2 / 正立面

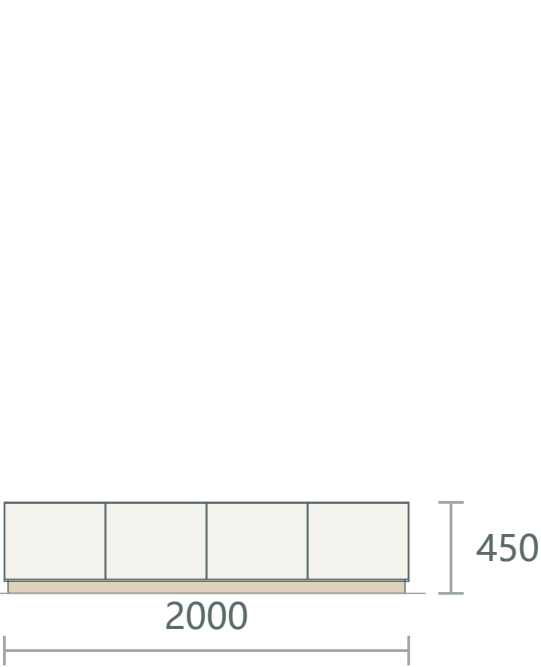


L2-U / 正立面




K5 / 正立面

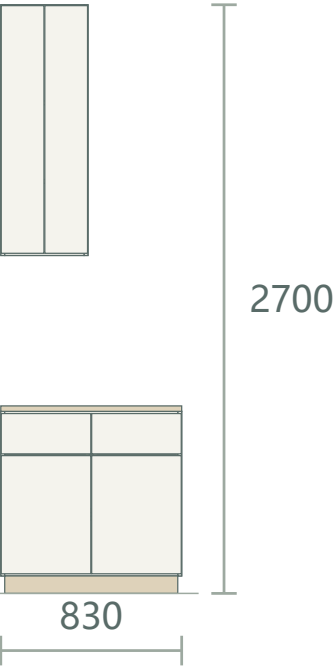


K3 / 正立面

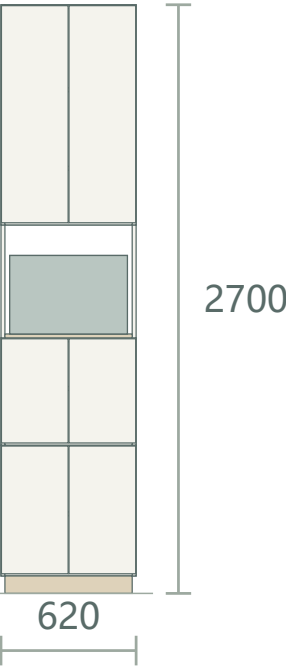

K4 / 正立面

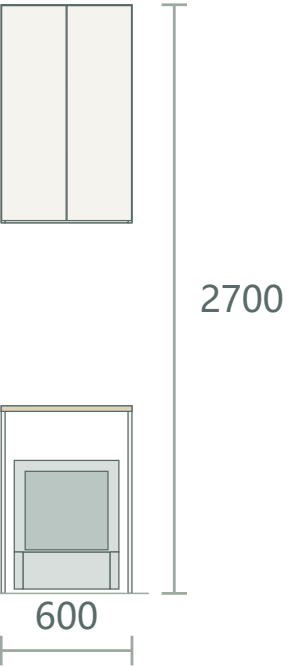


L2 / 去门板内部投影

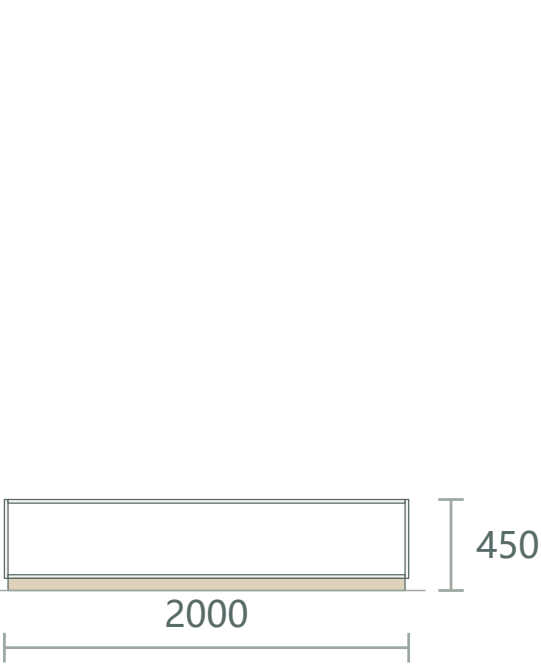


L2-U / 去门板内部投影




K5 / 去门板内部投影

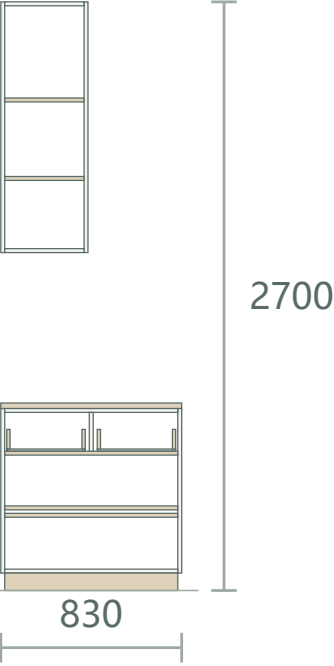

K3 / 去门板内部投影

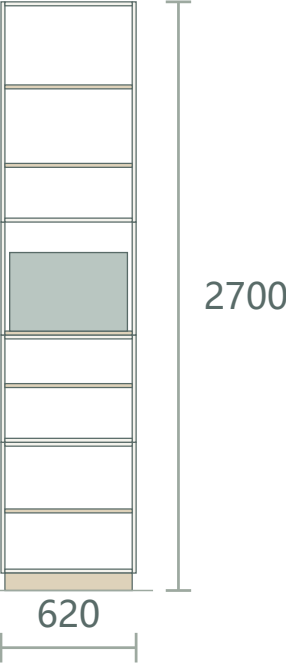


K4 / 去门板内部投影

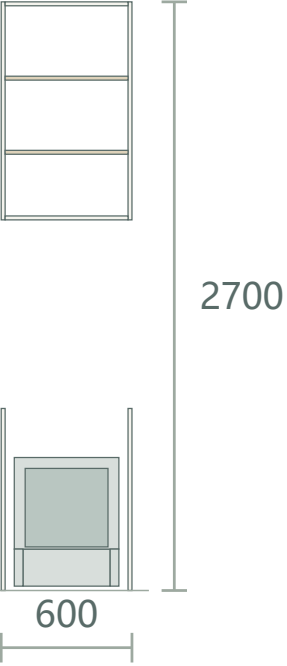

沿模型轴递增展开，非站位左右；标注柜体外包宽高，板厚为模型占位。内部去除门板和背板，非取消构件；不作为板件拆单。

电视墙立面定位

方案设计交付版 · 沿用R3设计条件 · 尺寸单位mm · 待现场复尺及厂家深化

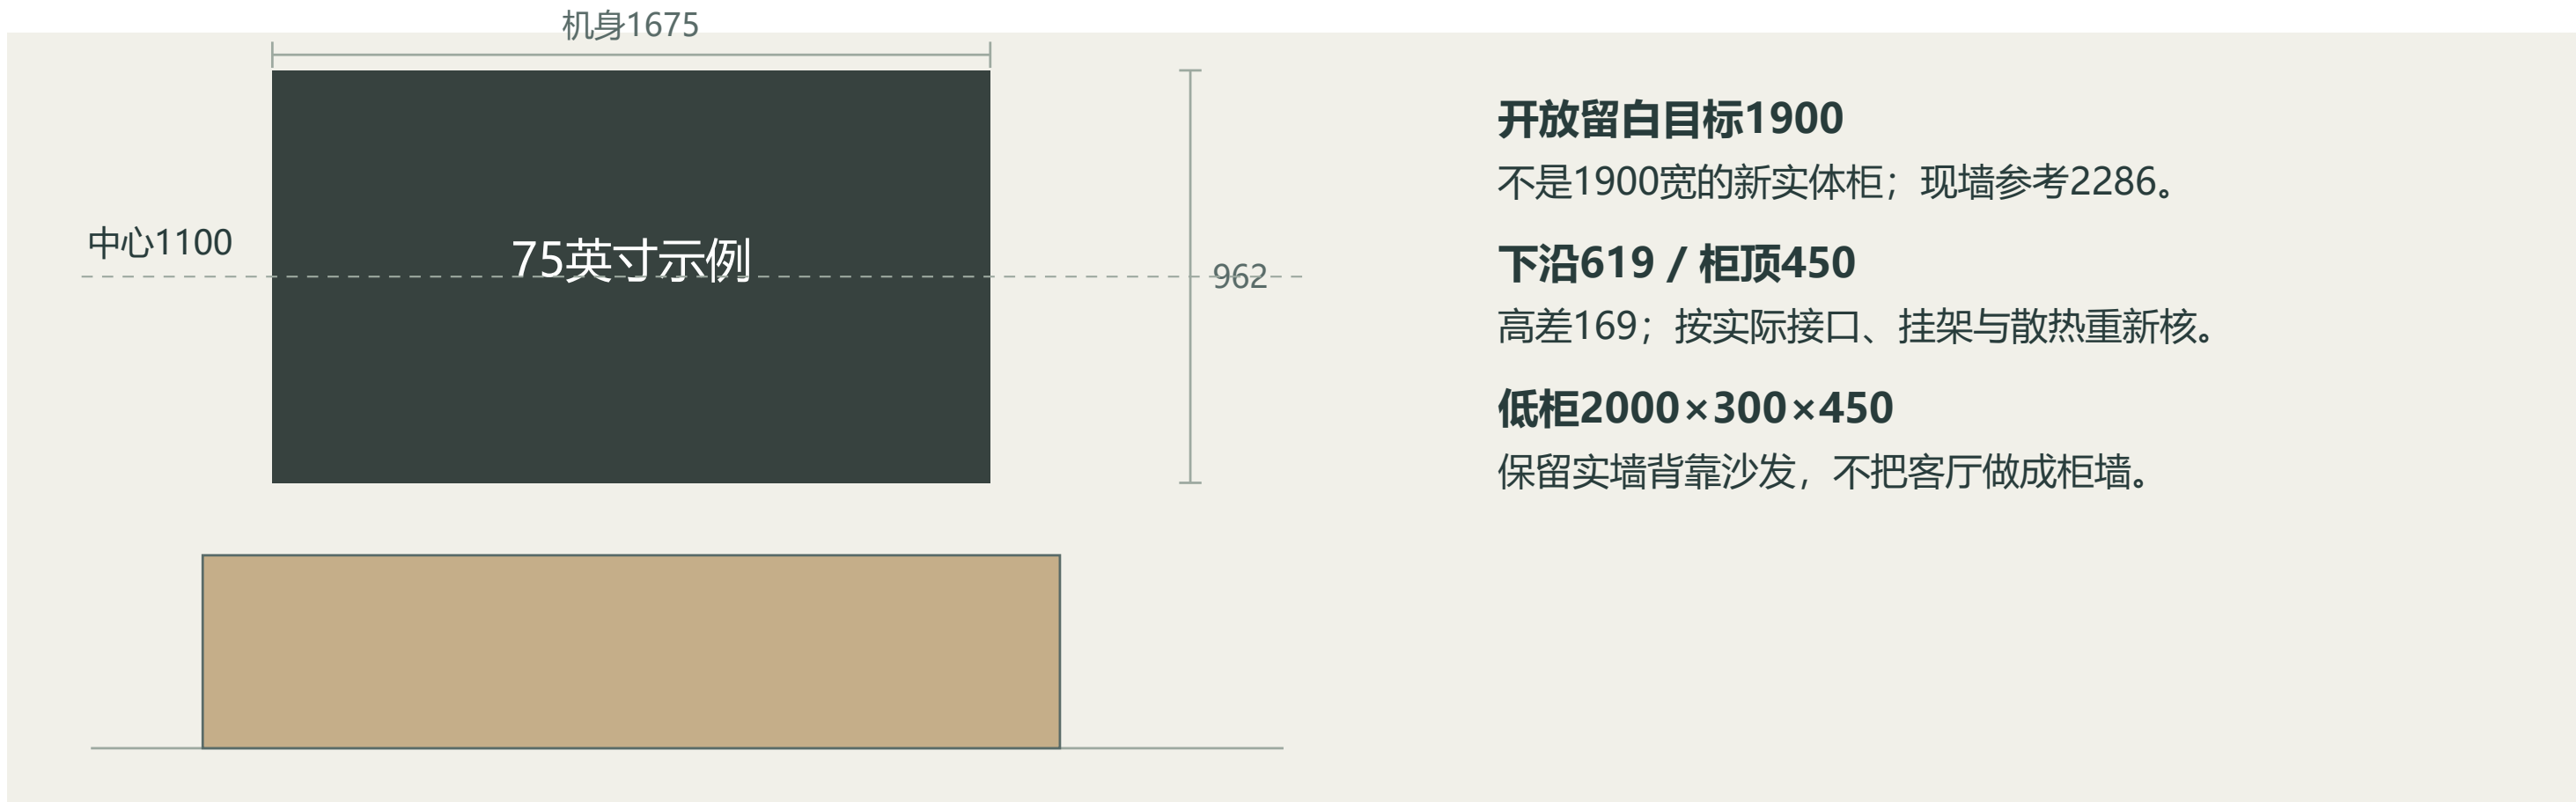

电视尺寸与观看轴线

参考墙长2286，75英寸示例机身1675×962，中心1100，下沿619，距低柜顶169；安装留白目标1900。与原沙发观看中心保持一致。最终按实际型号与坐姿调高低，不以英寸替代机身尺寸。

收纳与线材

遥控、游戏配件与纸品分可取盒；设备格需要通风，线管留可换线条件，插座不被固定背板封死。低柜现落地踢脚保留，不临时抬悬空后仍承诺同样容量或承载。

四人并坐的真实边界

四块约550净座位是紧凑并坐，不等于四张单人椅。保留小型可移边几，不追加贵妃位或大茶几。沙发靠实墙，背后不走人，坐位上方不新增深重柜。

依据 | G01 p8-11、16-19；75英寸示例来自用户已确认资料最新结论

餐厨服务带使用与设备控制

方案设计交付版 · 沿用R3设计条件 · 尺寸单位mm · 待现场复尺及厂家深化



三个不同的台面角色

K3储物；K4检修盖不能固定电器；K5仅临时落盘。

凯度若回退K3

原锅具区须重新分配，不能两种状态容量相加。

逐个开门装卸

不把冰箱、餐椅与机器人维护都算成同时可对穿。

K5浅餐边柜

830×350、台高860；两只浅抽净空目标约330×240×90，分餐具、餐巾与小件；下部活动板放杯碟。台面留临时放盘，不长期摆深度超出、蒸汽无法安全排放的小电器。

K3锅具与独立微波

K3下段作为灶下失去锅抽后的锅具库，先量锅柄最长尺寸与叠放高度。中段微波保持独立，按具体说明书决定开放格和散热；若凯度不能装灶下，K3须按原安装图另行转换，不能同时保留同体积锅具。

K4机器人与餐椅

机器人564几何净口仍待机型；上盖取水箱、尘袋、洗盘的路径不放电器堵死。餐椅拉出、冰箱开门、蒸烤取盘分别检查，不把多种状态同时画成双人可对穿。

依据 | G01 p8-11、17；G02 p12、66、72、95、102

厨房平面索引与空间示意

方案设计交付版 · 沿用R3设计条件 · 尺寸单位mm · 待现场复尺及厂家深化

01 / 空间平面与柜号



02 / 关闭外观



布置与使用要求

固定2247宽链；双槽、600洗碗机、米家烟灶保留。凯度灶下为条件方案，不是已批准安装。


读图及现场确认

平面编号与P-03、T-01/T-02对应；正立面按柜体朝向展开。三维图为剖墙示意，不是照片级效果图。尺寸和设备以本册控制值及复尺结果联合确认。


厨房柜体正投影展开

方案设计交付版 · 沿用R3设计条件 · 尺寸单位mm · 待现场复尺及厂家深化


K1 / 正立面

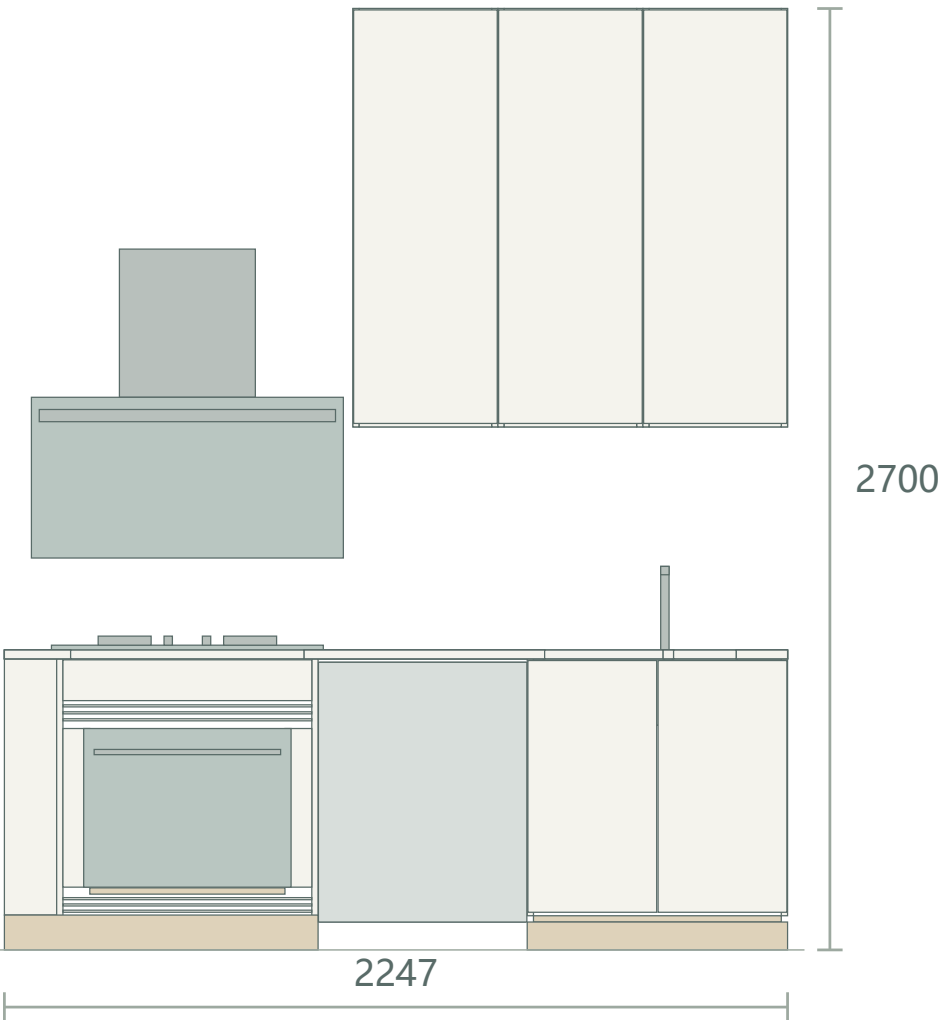

K1 / 去门板内部投影

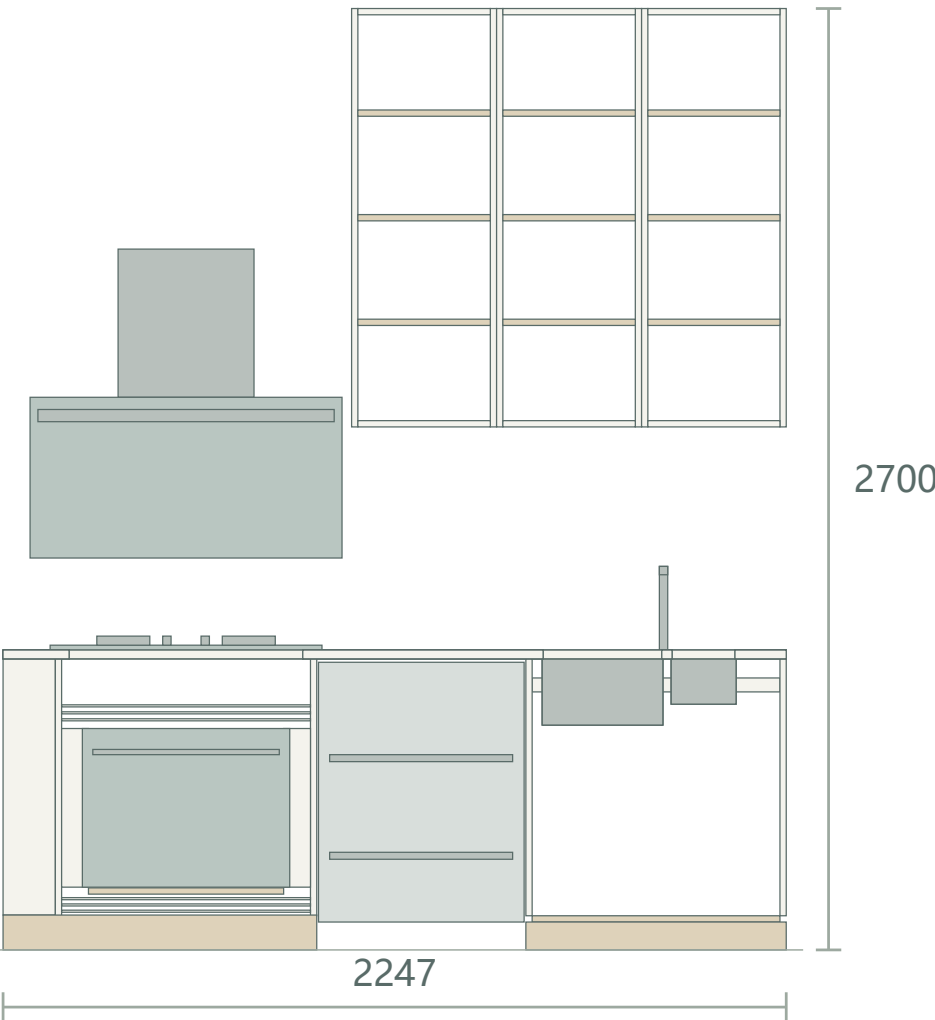

K1 / 侧向内部投影

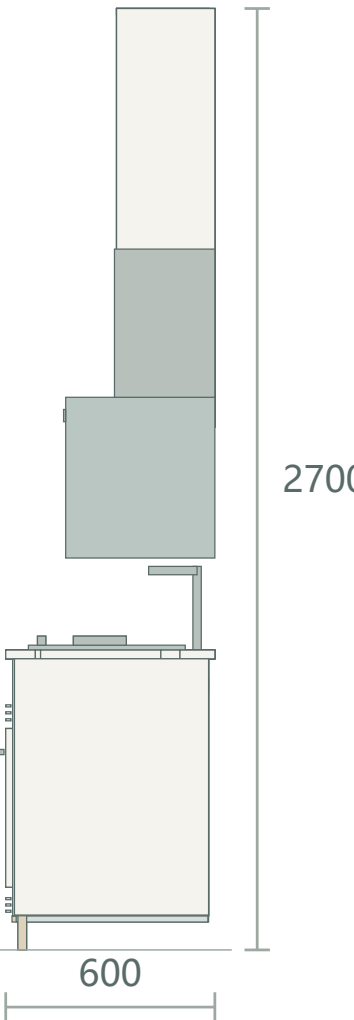

沿模型轴递增展开，非站位左右。侧向是内部投影，非施工剖切节点。标注柜体外包尺寸；内部去除门板和背板，非取消构件。

厨房台面与功能分段

方案设计交付版 · 沿用R3设计条件 · 尺寸单位mm · 待现场复尺及厂家深化

生活阳台侧 → 入口侧（展开端序，不表示站立左右）



洗、切、炒的连续台面

冰箱取物后送水槽清洗，转中间600备餐段，再到灶。600段不放电饭煲、台式蒸烤机或常驻沥水架；水槽可选可取沥水附件，不能盖住灶或把临时盖板当全天可用操作台。

工具按动作靠近

常用刀具/砧板在备餐侧收纳；锅铲调味靠烹饪侧，但避开炉火、烟机和可燃物禁区。重锅由K3低位取用，开火前备齐；吊柜只放轻物，不以升降篮增加未经验证的净容量。


不扩为L形或小岛台

当前单排与门窗边界不支持照搬指引的大型U/L型、岛台和高柜墙。保留可关闭厨房界面，门关闭控制油烟仍需必要新风和通风，不能封成密闭空间。

依据 | G02 p4、12、44、66、77-79、110、141

烟灶与凯度接口条件

方案设计交付版 · 沿用R3设计条件 · 尺寸单位mm · 待现场复尺及厂家深化

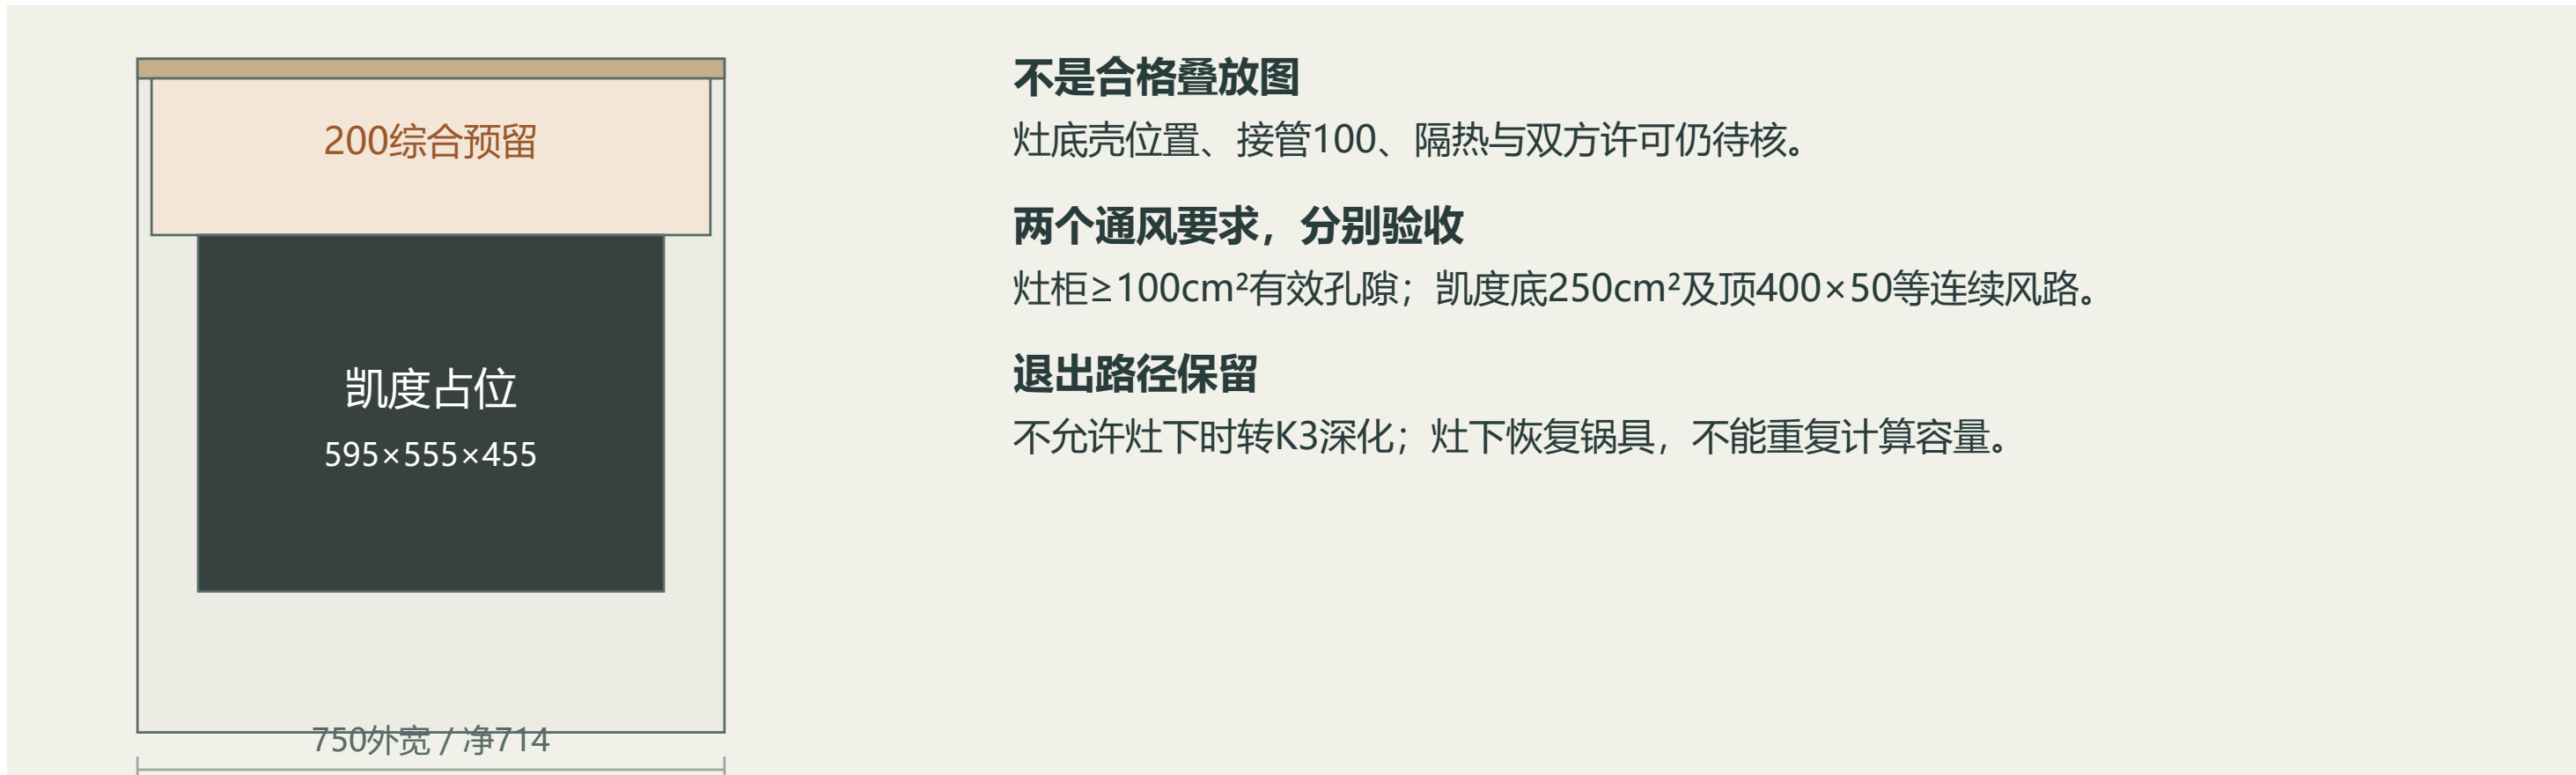

900烟机适配区不是机身净尺寸

按用户截图，吊柜组合宽900，机身示意宽895。图示690至760标注的两个端点必须按原安装图识别，不能自动当灶面到烟机最低点。烟道190、偏心32和离墙140按原图定位，不由柜体对称线猜位置。

凯度GR Pro仅尺寸候选

机身595×555×455，净孔560×至少540×450；底部250cm²通风口及上部400×50出口等按厂家安装图连续实现。600完成深不等于600安装净深；电源、接头和通风路径不占同一空间。


灶下是一条有退出条件的方案

机顶635到台底835的200空域并非合格证明。须双方允许组合，并核灶壳下探、灶底下100接管、隔热与阀门。用户灶图要求柜体有效通风不小于100cm²，必须与凯度要求分别落实，不能用一条装饰缝同时冒充满足。未通过转K3另行深化，保留独立微波。

依据 | 用户烟机/灶具两张安装图；凯度官方候选说明；G02 p24、59、130仅作参考

双槽联合湿区剖示

方案设计交付版 · 沿用R3设计条件 · 尺寸单位mm · 待现场复尺及厂家深化

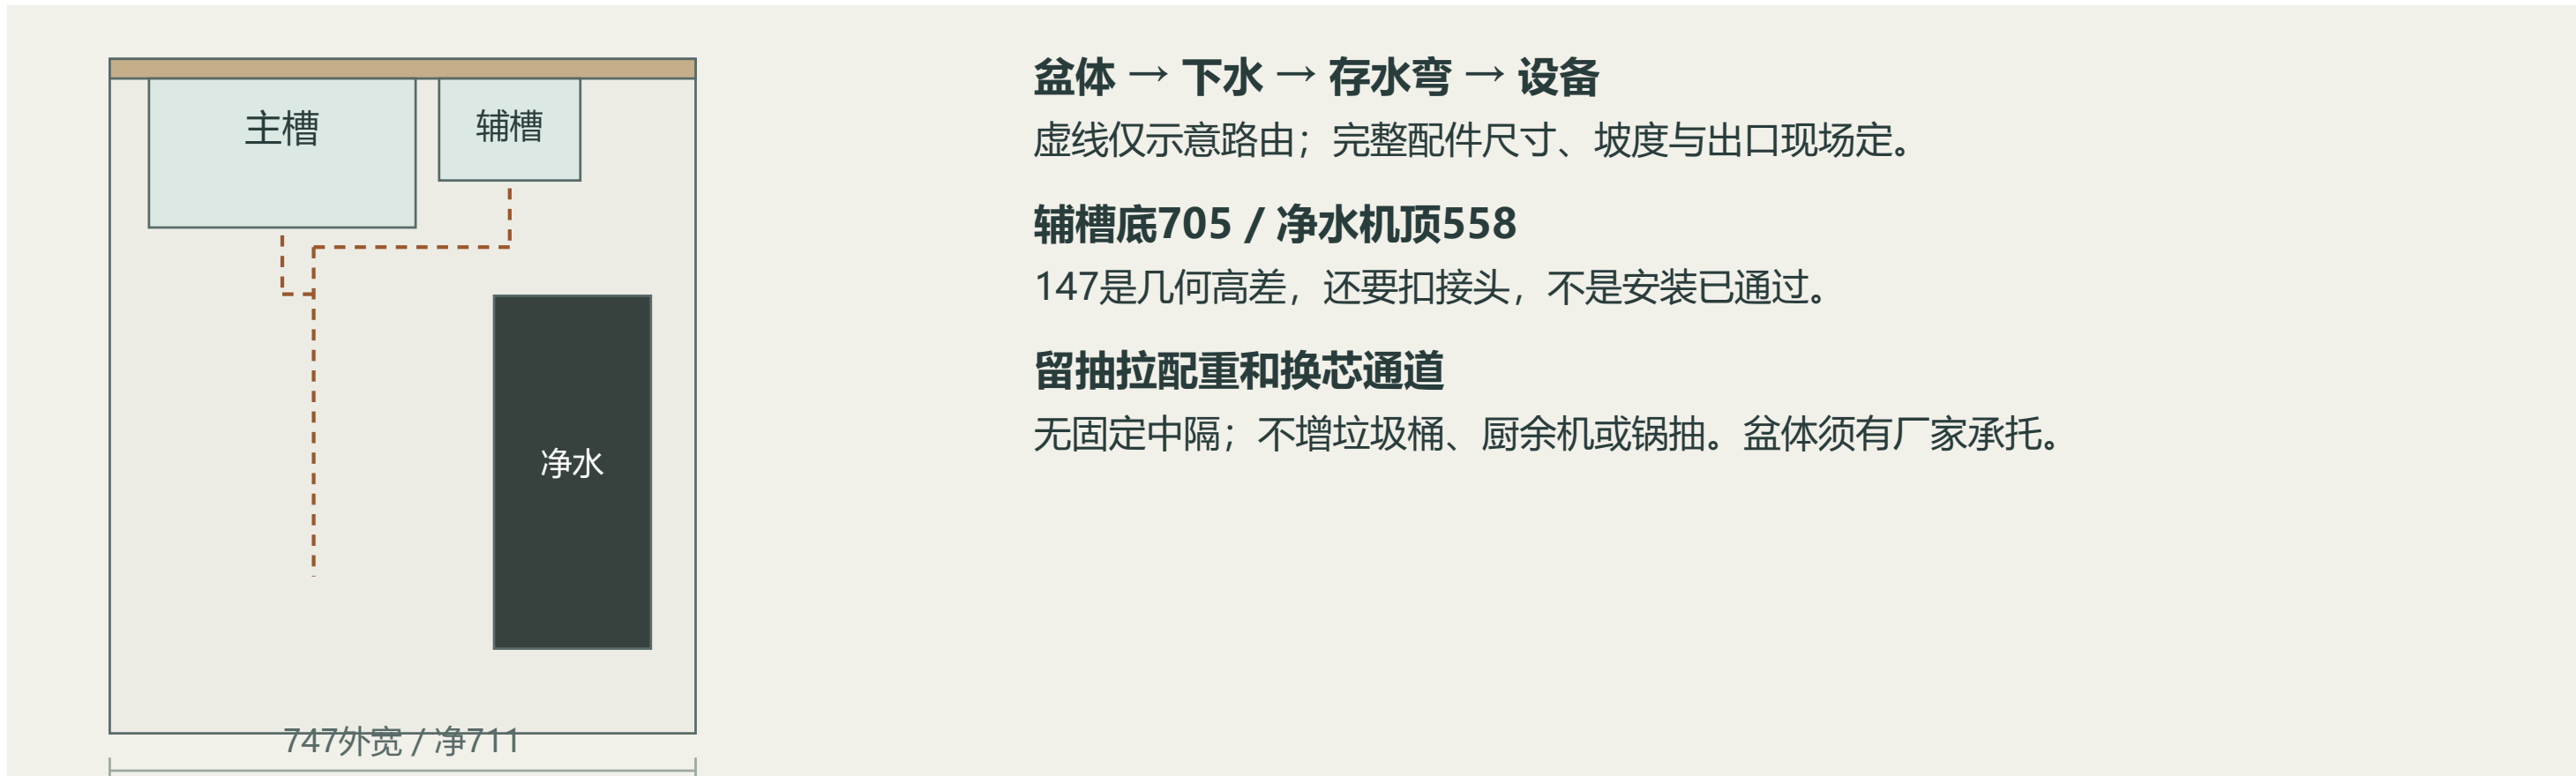

盆体 → 下水 → 存水弯 → 设备

虚线仅示意路由；完整配件尺寸、坡度与出口现场定。

辅槽底705 / 净水机顶558

147是几何高差，还要扣接头，不是安装已通过。

留抽拉配重和换芯通道

无固定中隔；不增垃圾桶、厨余机或锅抽。盆体须有厂家承托。

槽体与锅具试放

参考主槽340×400×190、辅槽180×400×130，槽体整体约585×440，仅作为比选体量。主槽靠备餐侧，浅辅槽靠入口侧。实际锅与锅柄、龙头摆角、盆夹和台面开孔模板必须一起核。

下柜不再叠加设备

净水器在浅辅槽下，排水优先主槽后侧；不得新增厨余机、内置垃圾桶、锅抽屉抢同一净空。可取接水盘与漏水提示作为深化项，盘不挡阀门和整机抽出。

垃圾位置另做使用测试


日常小垃圾容器须在不挡门、不压备餐台的位置实试；当前不承诺柜内垃圾分类系统。双槽、净水、存水弯各有体积和拆卸路径，检修时停用水电并由相应人员处理。

依据 | G02 p4、13、39、42、64、65、73、130


主卧平面索引与空间示意

方案设计交付版 · 沿用R3设计条件 · 尺寸单位mm · 待现场复尺及厂家深化

01 / 空间平面与柜号

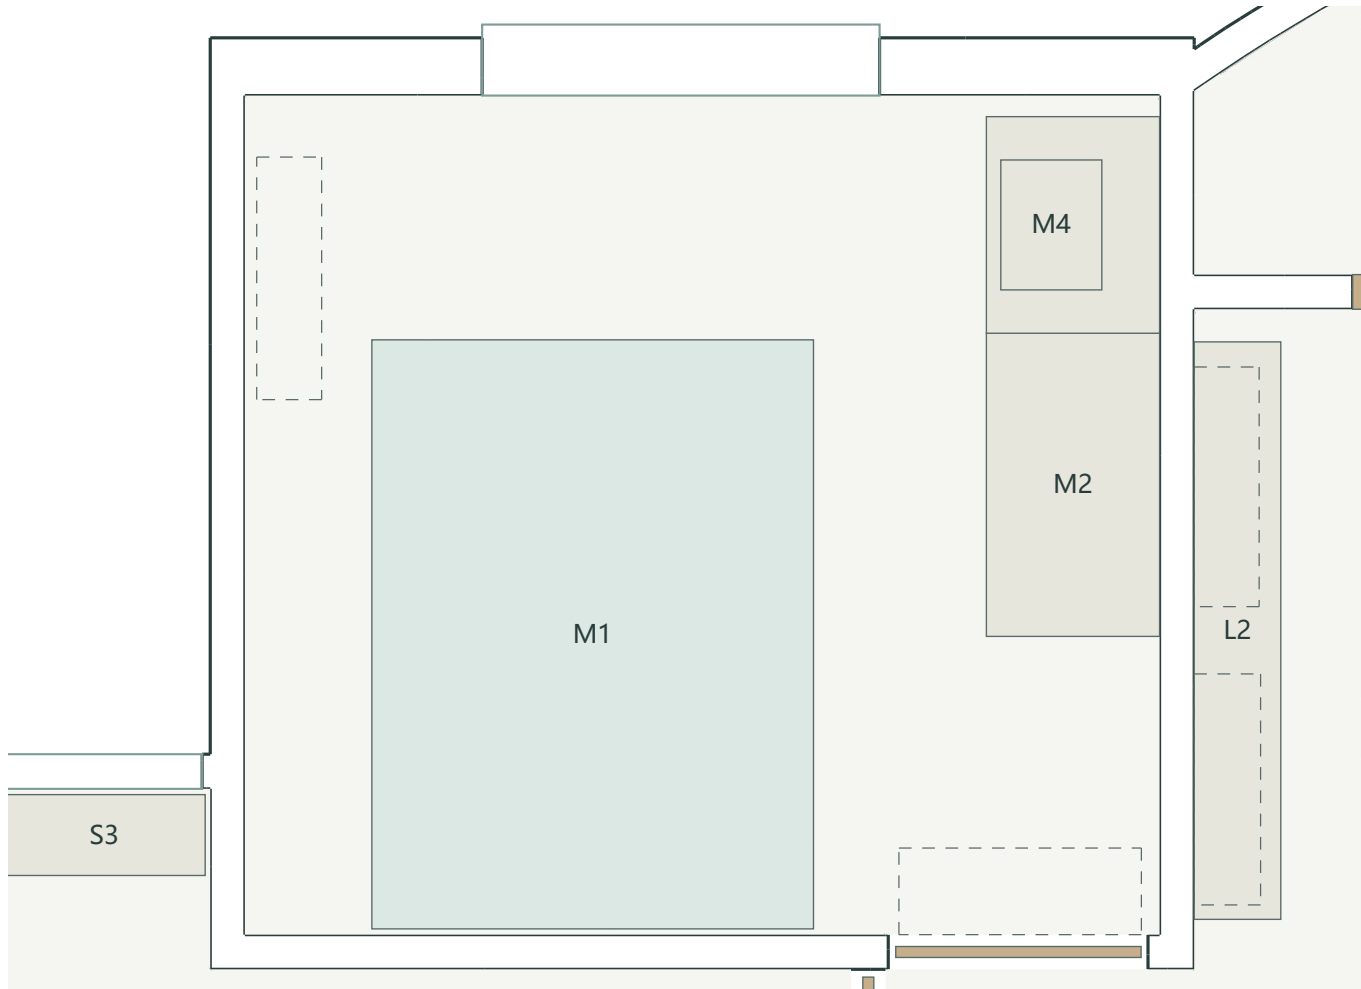

02 / 关闭外观

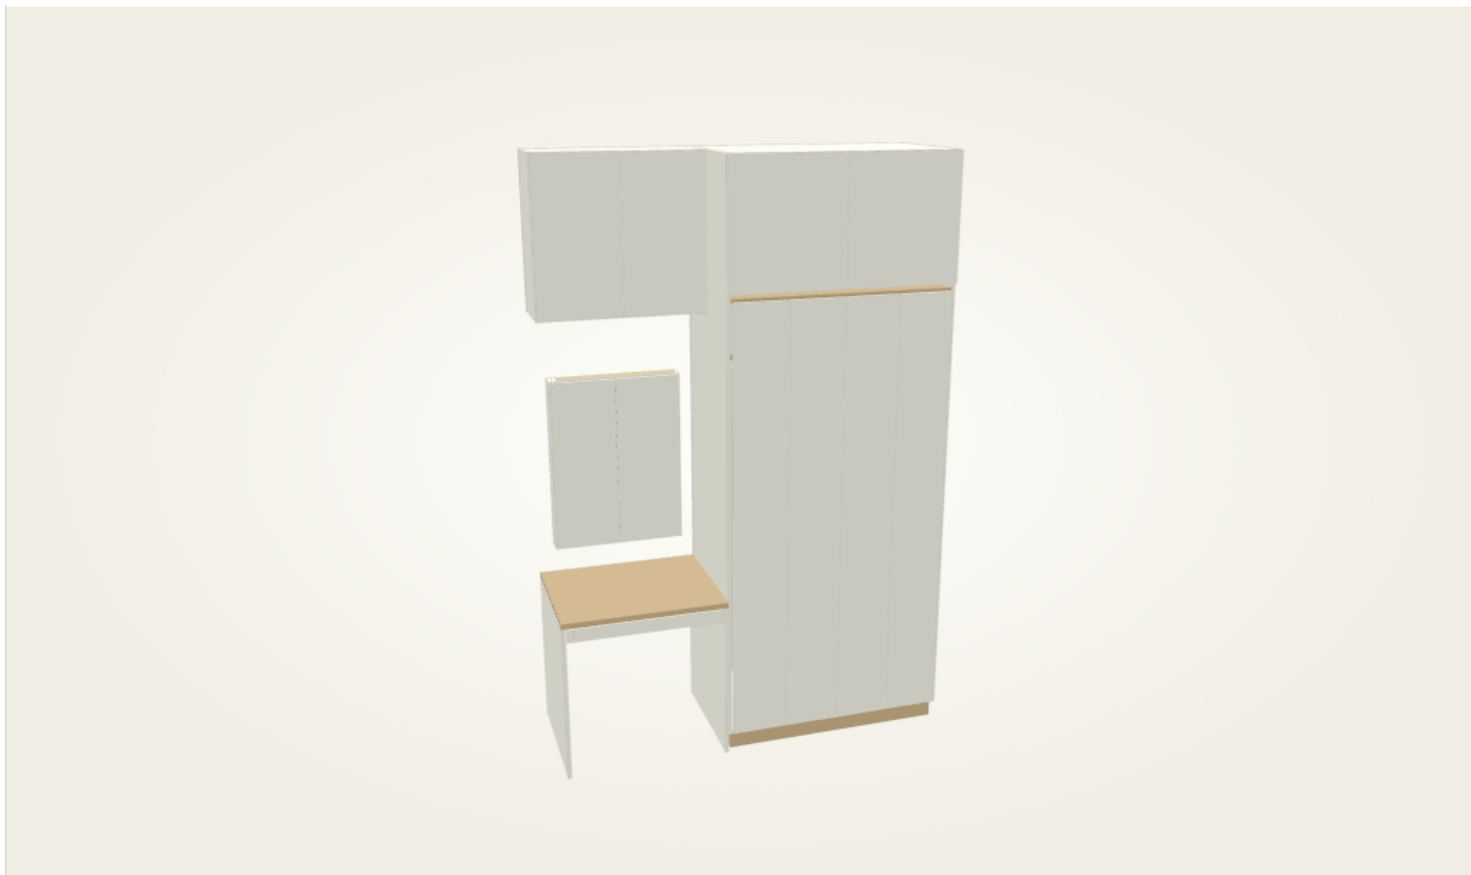

布置与使用要求

保留1500×2000床垫和实体床头；关闭态柜前599、床侧440为参考窄点。镜可关闭，床头无深重吊柜。


读图及现场确认

平面编号与P-03、T-01/T-02对应；正立面按柜体朝向展开。三维图为剖墙示意，不是照片级效果图。尺寸和设备以本册控制值及复尺结果联合确认。


主卧柜体正投影展开

方案设计交付版 · 沿用R3设计条件 · 尺寸单位mm · 待现场复尺及厂家深化

M2 / 正立面

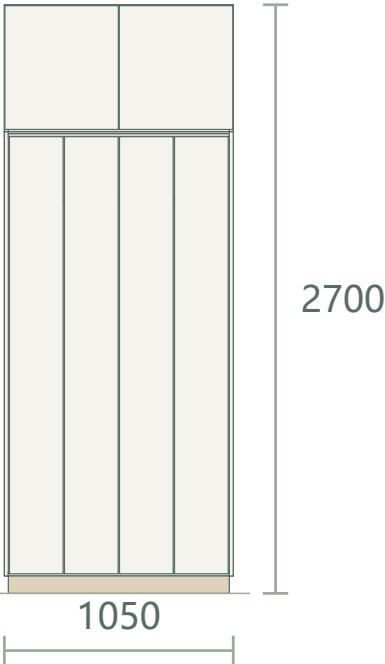


M3 / 正立面

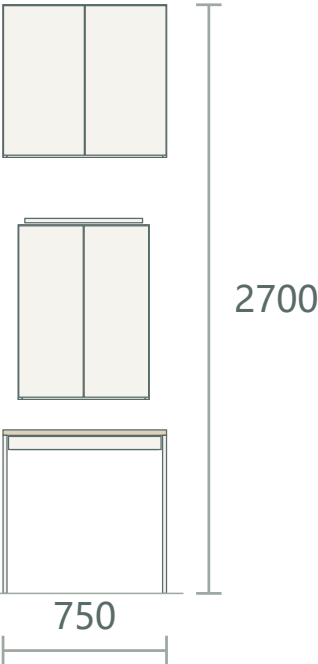


M5 / 正立面



M2 / 去门板内部投影

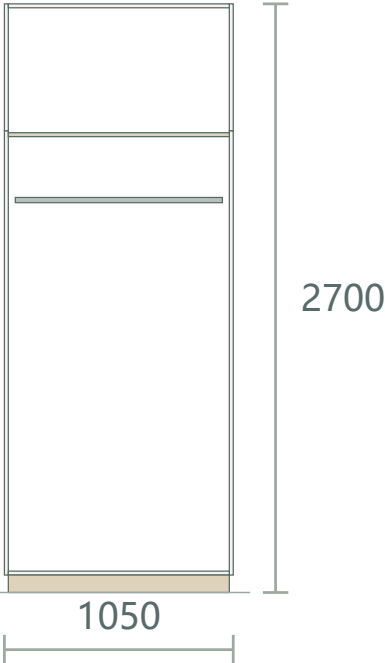

M3 / 去门板内部投影

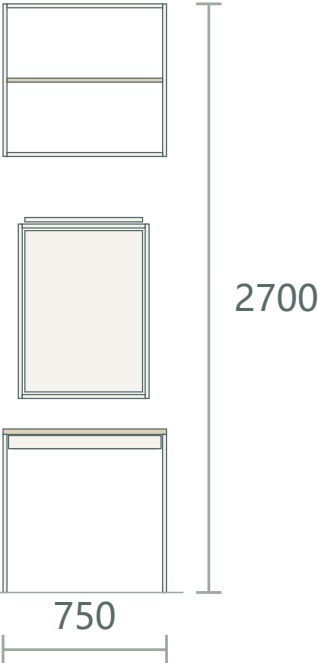

M5 / 去门板内部投影



沿模型轴递增展开，非站位左右；标注柜体外包宽高，板厚为模型占位。内部去除门板和背板，非取消构件；不作为板件拆单。

M2衣柜挂衣尺寸控制

方案设计交付版 · 沿用R3设计条件 · 尺寸单位mm · 待现场复尺及厂家深化



常用衣物更易取挂

主杆中心由1910降到1800, 保留1750至1910可调位置。底板顶98, 杆中心至板顶1702、杆下缘至板顶1690, 未扣衣架与下摆余量, 不宣称可挂1700长衣。模型衣片改1600高、顶1730, 只是几何示意, 不代表实物已适配。

底盒默认移出

原430×350×220底盒不再占长衣下方, 低频软物转床箱或上柜, 实际容量相应转移。以后若放回底盒, 杆中心到盒顶仅1482, 必须重新核衣长, 不能一边放盒一边沿用1702。

599不是宽敞通道

指引案例建议柜床间600以上, 现模型599属于临界, 左床侧440也偏紧。保留窄幅联动折门, 按真实门厚、折叠停车、手位与衣架做1:1样板; 不为凑1毫米挤另一侧, 也不承诺普通平开深抽都能用。

依据 | G06 p8、10、21、109

M3梳妆位与可关闭镜面

方案设计交付版 · 沿用R3设计条件 · 尺寸单位mm · 待现场复尺及厂家深化



台面750 / 膝净高目标 ≥ 650


薄抽不加厚；腿部净深目标450至550。

上柜底2000 / 深300

轻物上移，不做低吊柜压头。

镜盒600 $\times$ 100 $\times$ 800

镜门关上后不照床；光从两侧均匀照脸。

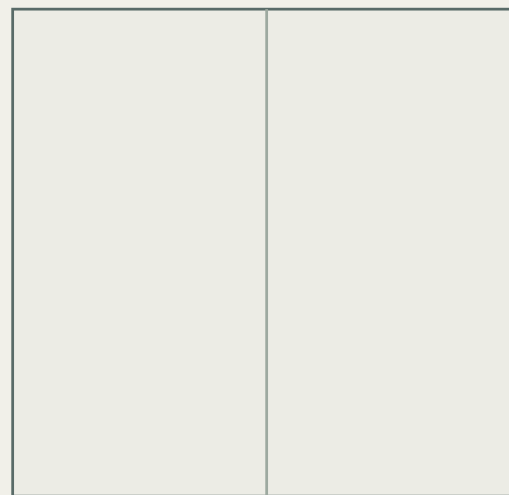

关闭镜盒示意

腿部与薄抽不互相挤占

台下膝净高目标至少650、腿部净深450至550；750高包含台板，不再在台下加整排厚抽。保留700 $\times$ 300 $\times$ 60外包薄抽及250示意行程，坐凳用后完整归位，床尾取物与梳妆分时。

镜盒和侧向面光

600 $\times$ 100 $\times$ 800可关闭镜盒保留，关闭时无外露镜面照床。两侧或均匀正面补光，避免只在头顶照出阴影；驱动、插座和连接可维护，充电器不压在衣物下。


日式留白不等于空着不用

台面只放当天用物；首饰化妆工具进可取小盒，备品入上柜。开放位不再塞大展示柜或L形外伸桌，原1800衣柜梳妆组合长度不扩张。

依据 | G06 p24、34、43–44、47–48、75、78、135、143；用户已确认资料可关闭镜面要求

床与飘窗高度关系

方案设计交付版 · 沿用R3设计条件 · 尺寸单位mm · 待现场复尺及厂家深化

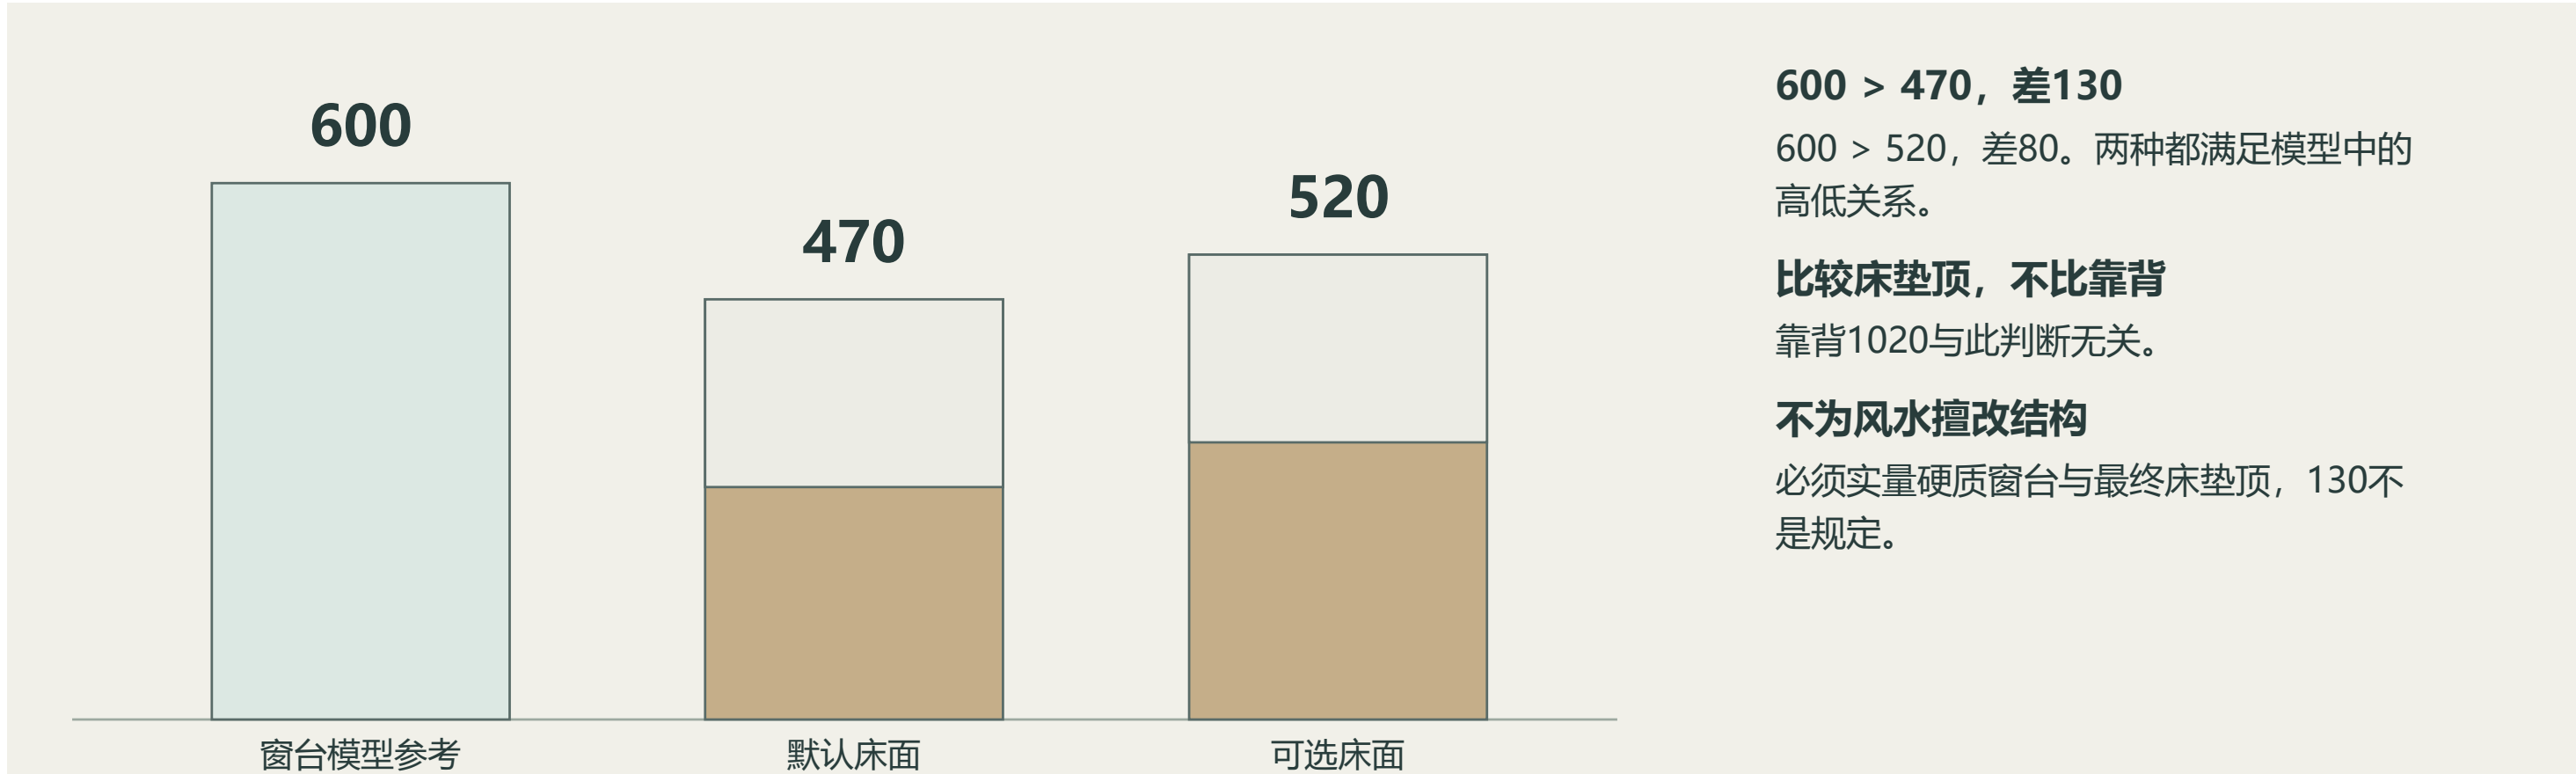

本轮保留两套高度

网页默认470 = 承托260 + 床垫210，高差130；可切回520 = 310 + 210，高差80。两者按参考模型均满足你的要求。靠背1020不纳入床垫面比较，130不是风水规定。

舒适与容量一起选

470床减少50床箱高度，抽屉仍须核轨道和板件；520更易保留原收纳。用实际床垫和身高试起坐后确定，不只为了图面高差挑最低床。窗边不新做深柜、坐榻或向外扩窗。

不能替代防坠核验


窗台高于床不意味着临空外窗已安全；护栏、开启限位、可登踏面及固定由现场专业核。原模型窗构件厚246不是可坐台面净深，也不是允许拆除的结构证明。

依据 | G06 p24、29-31、77-78；原DAE窗下墙体顶面；用户床窗高低要求


次卧平面索引与空间示意

方案设计交付版 · 沿用R3设计条件 · 尺寸单位mm · 待现场复尺及厂家深化

01 / 空间平面与柜号

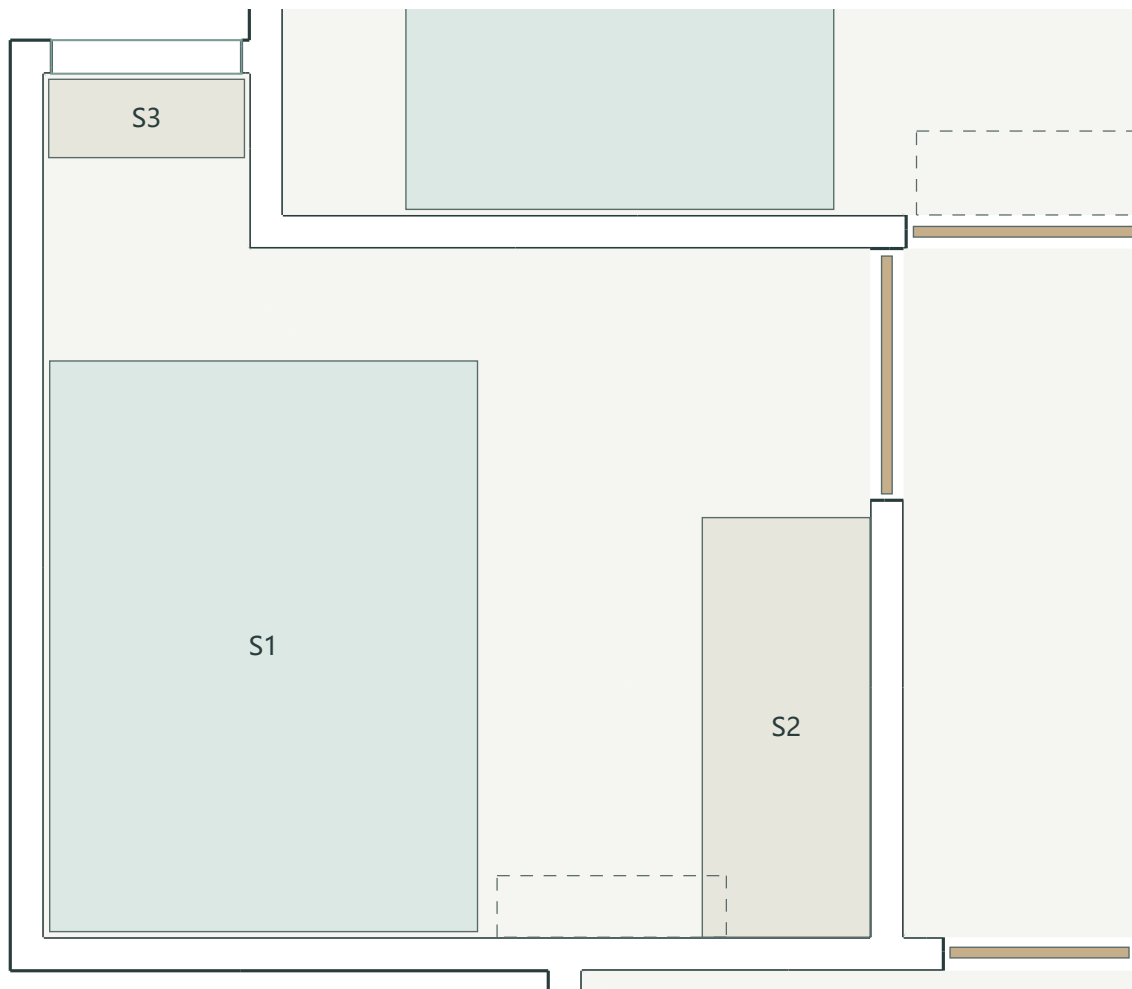

02 / 关闭外观

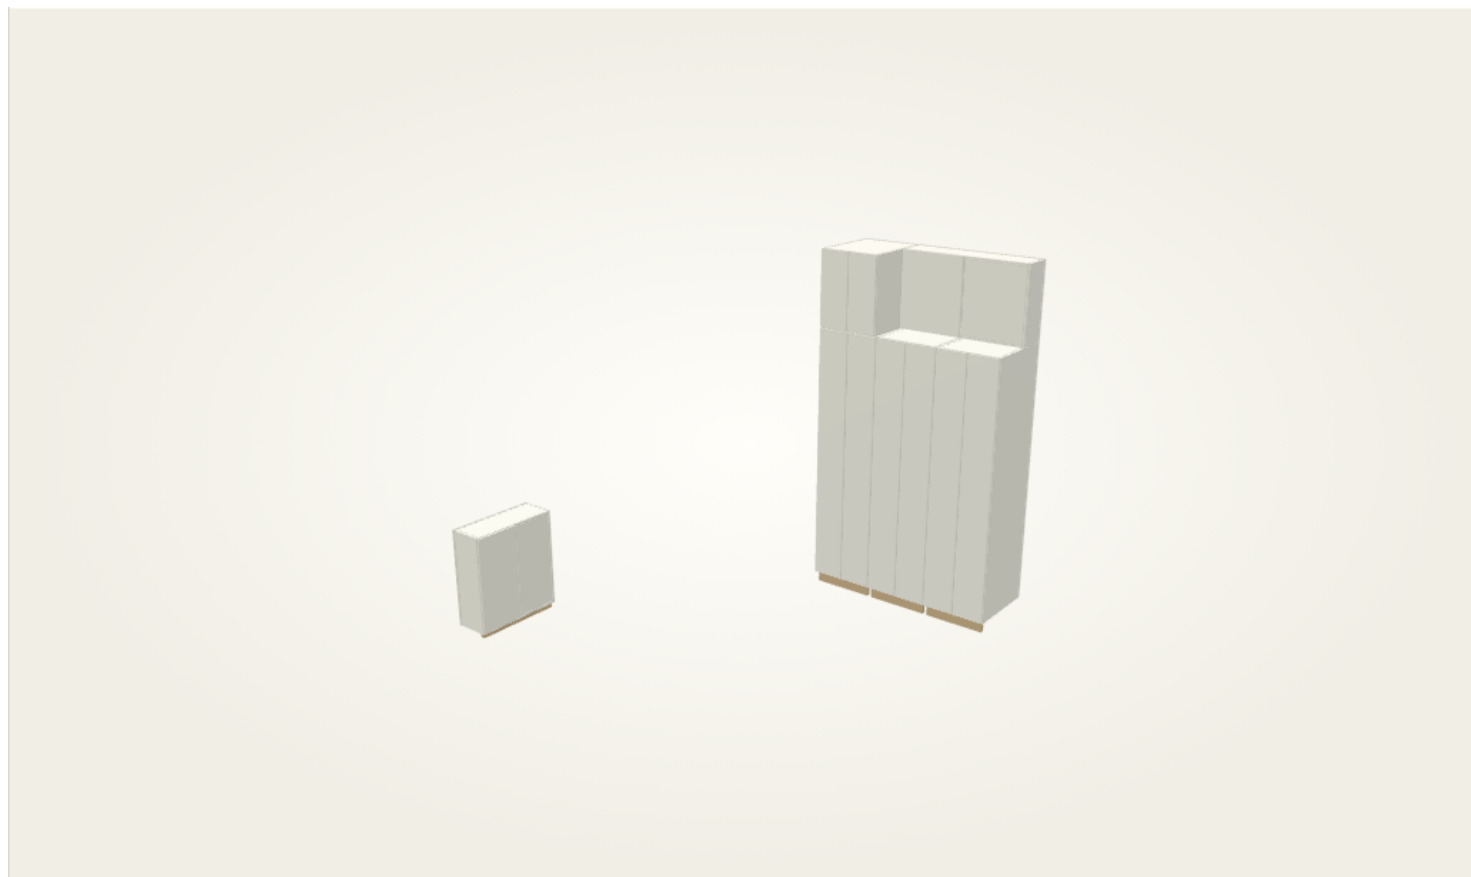

布置与使用要求

保留固定1500×2000床；柜前804、床尾进入窄点402，不表述为舒适通道。保留空调检修退台。


读图及现场确认

平面编号与P-03、T-01/T-02对应；正立面按柜体朝向展开。三维图为剖墙示意，不是照片级效果图。尺寸和设备以本册控制值及复尺结果联合确认。


次卧柜体正投影展开

方案设计交付版 · 沿用R3设计条件 · 尺寸单位mm · 待现场复尺及厂家深化


S2 / 正立面

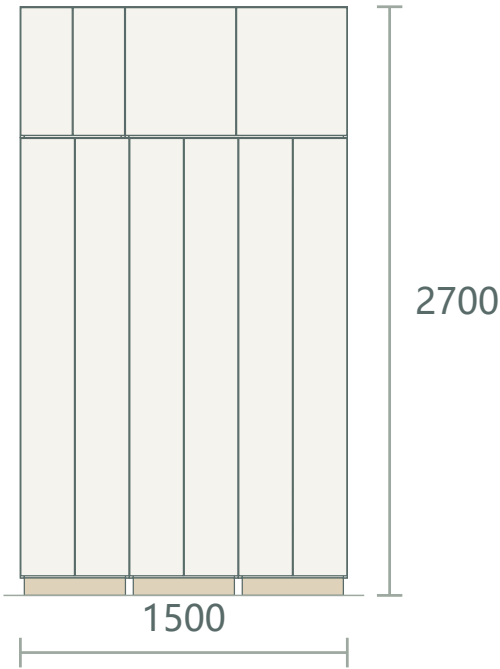


S2 / 去门板内部投影

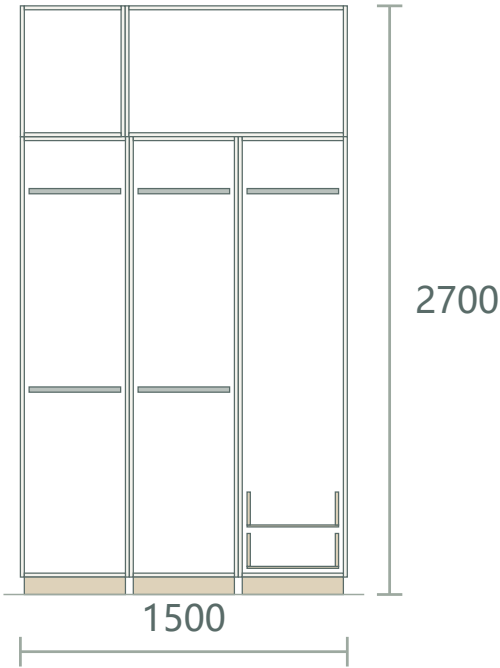

S3 / 正立面

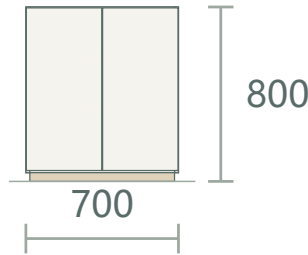


S3 / 去门板内部投影

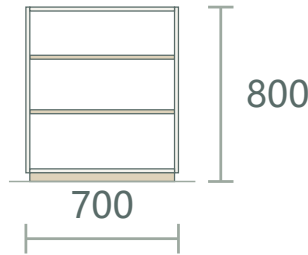

沿模型轴递增展开，非站位左右；标注柜体外包宽高，板厚为模型占位。内部去除门板和背板，非取消构件；不作为板件拆单。

S2衣柜分格尺寸控制

方案设计交付版 · 沿用R3设计条件 · 尺寸单位mm · 待现场复尺及厂家深化

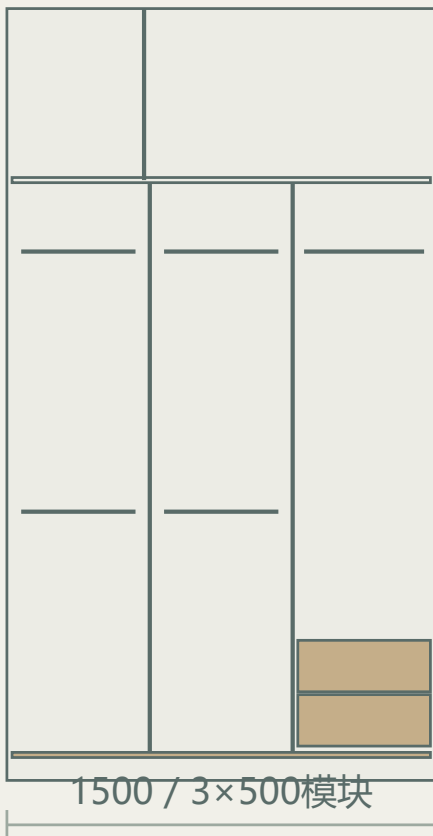

上杆1850 / 下杆940

原1900/990各降50；上、下中心距仍910。

下层约束更严格

下杆中心到底板842、下缘830，再扣衣架。

第三格不变

单杆1850 + 两浅抽；超长衣转主卧。

顶部退台不填满

480宽深600 + 1020宽深250，留空调。

窄点仍存在

柜前804、床尾402、靠墙侧21。门抽分时开启。

没有增加总柜量

优化取挂，而非凭示意衣片声明容量增长。

两组双挂1850/940

上、下杆同时降低50，杆中心距仍910；下杆中心至98底板842，杆下缘至板顶830，再扣衣架及下摆。短上衣实挂不合适就调回1900/990或撤一根杆，不把长外套硬算进双挂。

单挂与浅抽保留

第三格主杆1850和两只浅抽不变，超长衣转主卧。三个500模块理论净宽各464；内抽需扣门铰与侧垫，不能用箱体净宽当抽屉净宽。浅顶柜净深约194，只放薄盒。

402窄颈明确保留

柜前804是关闭态；靠墙侧约21不走人，床尾402只是进入窗凹位的窄点，不称舒适主通道。衣柜、内抽和床侧抽屉分时开，不加固定书桌或落地床头柜。

依据 | G06 p8、10、18、21、83、109

设计阶段：方案深化 / 非生产下料图

未复尺尺寸以参考模型为依据；禁止据图直接开孔、接管或改结构。

比例：示意 / 不按图量取

图幅：A3横向 / 缩放打印比例失效

版本：R4 / 2026-09-30


设计基线：交互模型R3

图号：S-03

页次：29 / 50

S3窗下柜与空调避让

方案设计交付版 · 沿用R3设计条件 · 尺寸单位mm · 待现场复尺及厂家深化

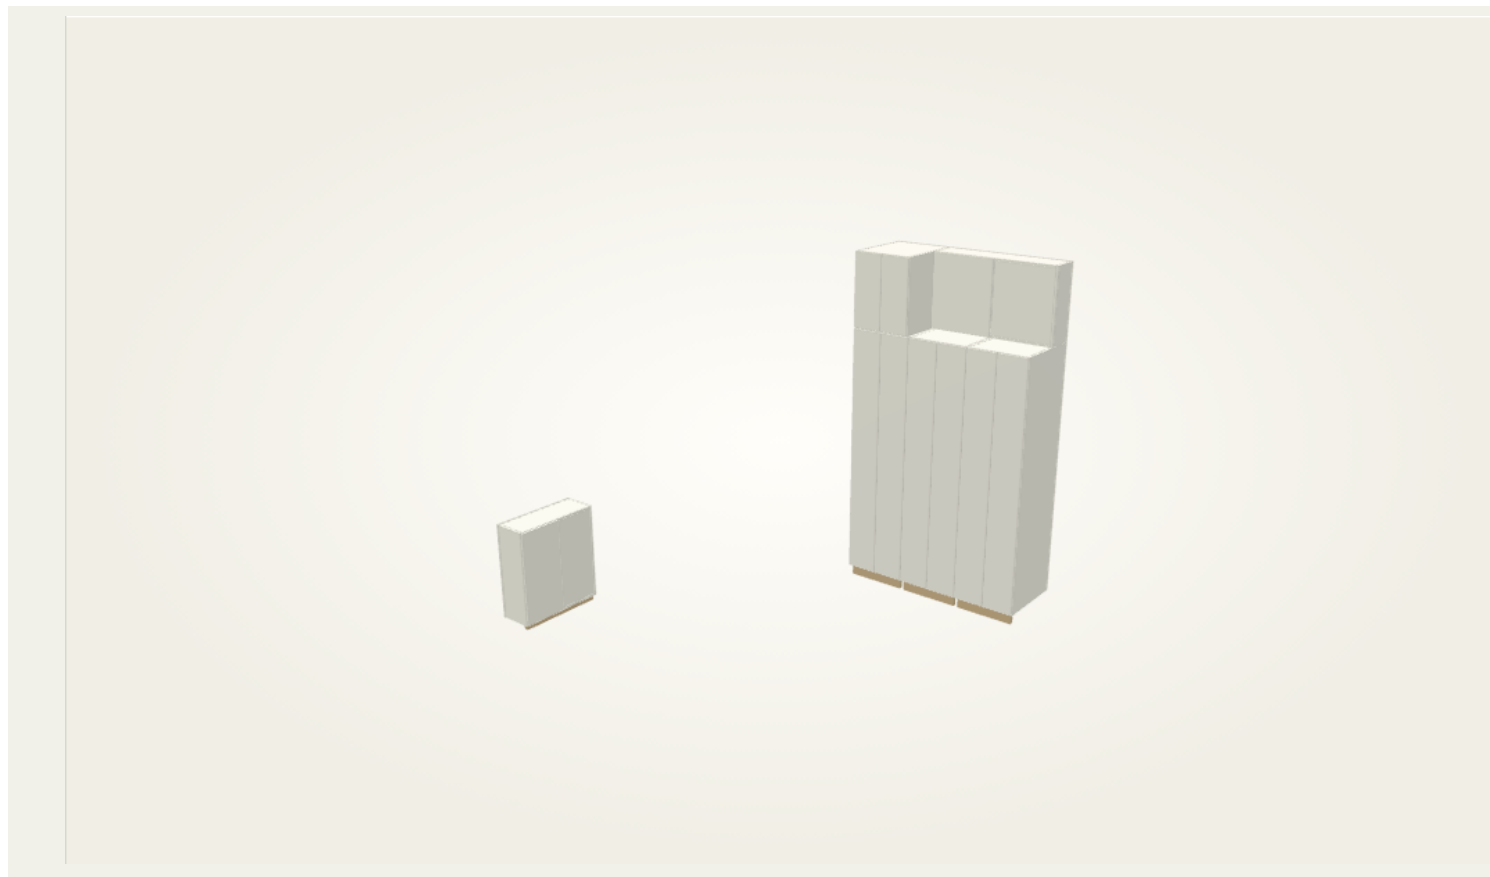

窗下柜700×280×800

窗底参考900；柜顶不当踏台。

理论净深224

实物还要能通过单侧移门口，不能只看664总内宽。

空调在靠厨房方向墙

保滤网抽取、检修、送风；不将窗凹位改整排榻榻米。

低频浅收纳

两扇移门与活动层板保留，理论浅净深约224；放薄盒、纸品和季节小物。窗执手、窗扇、卷帘和清洁手位实量后再定层板，不在800柜顶加厚软垫诱导攀坐。

空调空间不重新填满

次卧挂机在靠厨房方向墙，邻近上柜维持480宽深600+1020宽深250退台；不把机体或检修带算成收纳。滤网取出、送风、冷凝水和维修按具体机型核。

风水与采光


床头仍实墙约东南，镜面不新朝床；不为增加一格柜封窗、压枕或拆改外窗。主卧窗台600与次卧窗底900属于不同位置，不能混用。

依据 | G06 p10、17、21、77；既有空调检修退台与窗模型


卫浴平面索引与空间示意

方案设计交付版 · 沿用R3设计条件 · 尺寸单位mm · 待现场复尺及厂家深化

01 / 空间平面与柜号

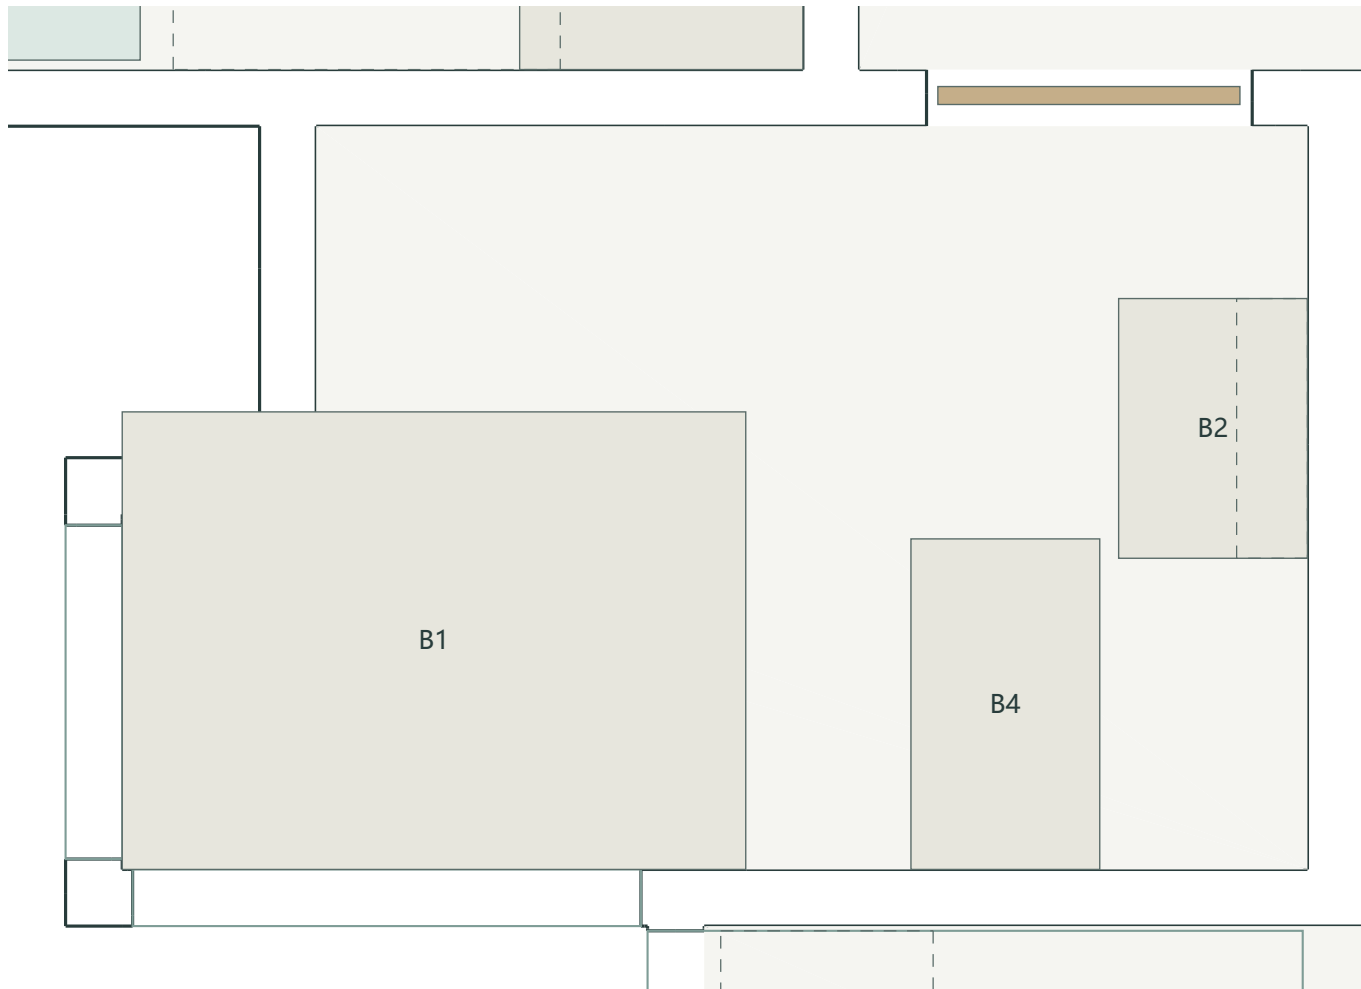

02 / 关闭外观

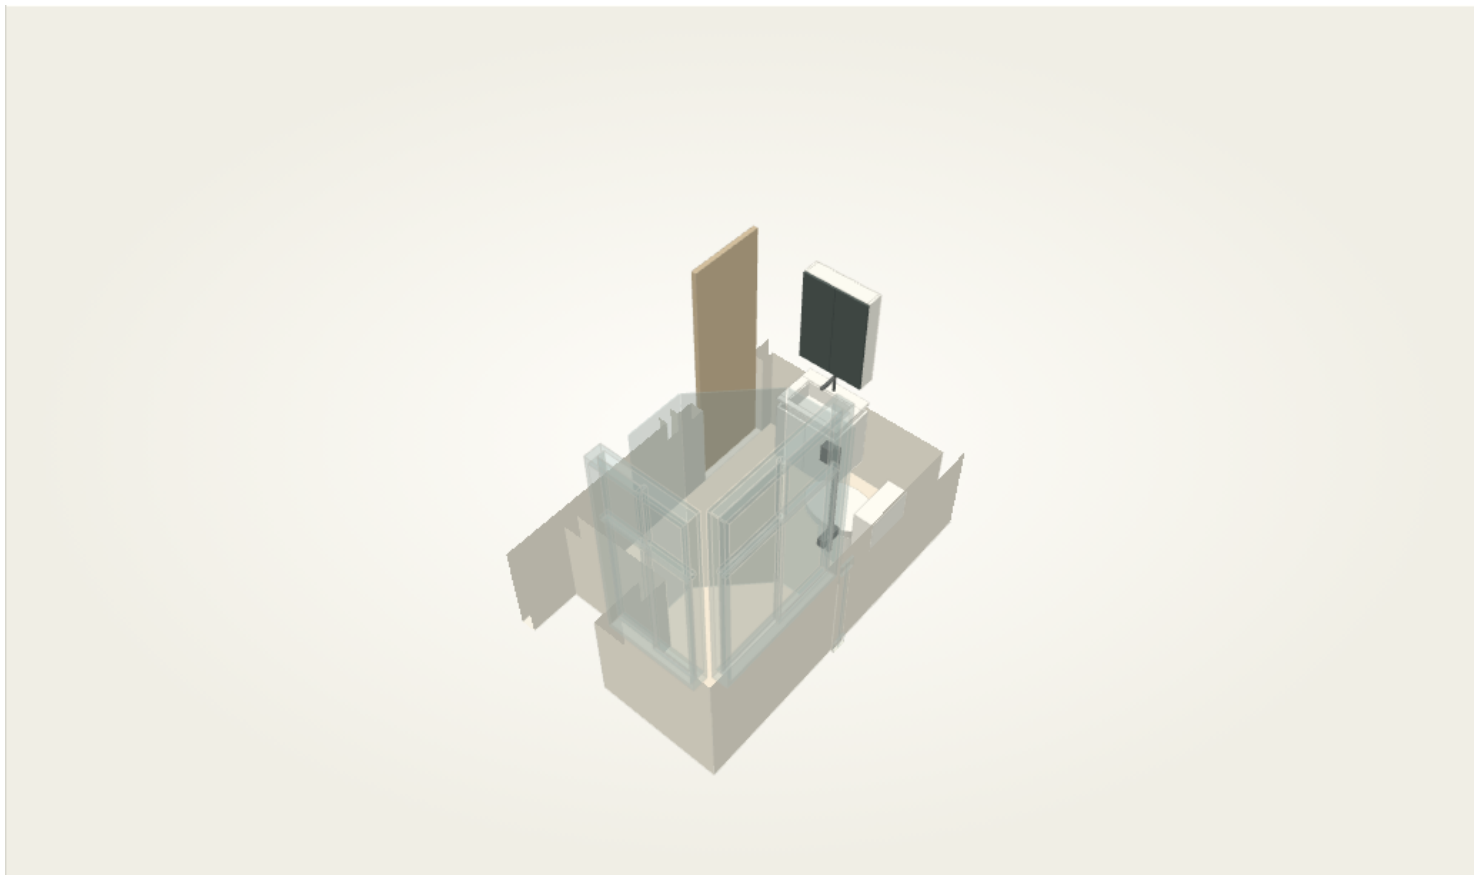

布置与使用要求

保持原排污和浅盆方案，门位冲突须先复尺；盆前凸量、淋浴入口及门扇扫掠单独核。


读图及现场确认

平面编号与P-03、T-01/T-02对应；正立面按柜体朝向展开。三维图为剖墙示意，不是照片级效果图。尺寸和设备以本册控制值及复尺结果联合确认。


卫浴柜体正投影展开

方案设计交付版 · 沿用R3设计条件 · 尺寸单位mm · 待现场复尺及厂家深化


B2 / 正立面

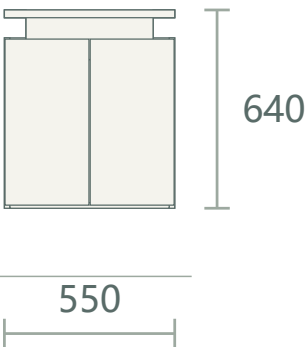


B2 / 去门板内部投影

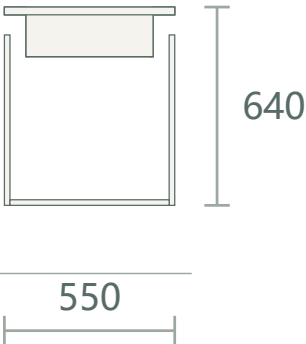

B3 / 正立面

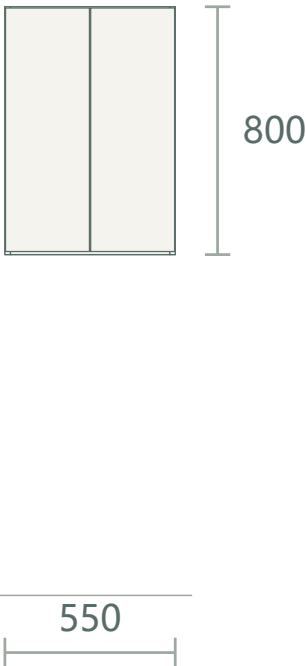

B3 / 去门板内部投影

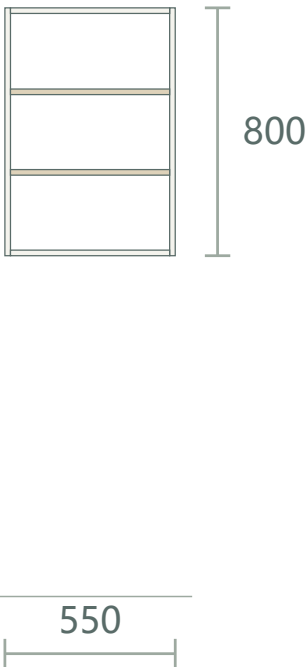

沿模型轴递增展开，非站位左右；标注柜体外包宽高，板厚为模型占位。内部去除门板和背板，非取消构件；不作为板件拆单。

卫浴净空与淋浴入口控制

方案设计交付版 · 沿用R3设计条件 · 尺寸单位mm · 待现场复尺及厂家深化



651与665不是同一口径

内参考460切角斜边≈651；外轮廓470切角≈665。640门叶不等于净入口。

浅盆550×400仍须试样

如用前凸半嵌盆，以最前盆沿重算站位和门扇扫掠。

真实门位优先

20楼门位与二维图冲突未定，外开门、后退盆保持条件状态。

浅盆柜保留而非扩深

550×400盆柜后退方案保留，优先试合适的盆形、龙头高度和落水点。指引400深半嵌盆示例有前凸：400柜深不等于盆最前缘总深，必须把实际前凸计入通道；防溅和洗脸站姿用1:1实物试。

切角淋浴与门

900×959为内侧参考包络，切460×460约损失0.106㎡；其斜边约651。模型外轮廓为470×470切角、斜边约665；640门叶不等于净入口。厂家按实配型材、铰链、把手核净口，不以切角形状判断吉凶。


门位冲突处理

浴室主门外开、限位与盆柜后退先按参考模型；若20楼为二维图另一门位，必须联动重排，不沿用卧厕门对冲结论。马桶优先原排污，不为布局吉位做未经核验的长距离移管。

依据 | G03 p6、82、86、90、95；淋浴数值来自参考模型内外口径

盆柜与镜柜分格控制

方案设计交付版 · 沿用R3设计条件 · 尺寸单位mm · 待现场复尺及厂家深化

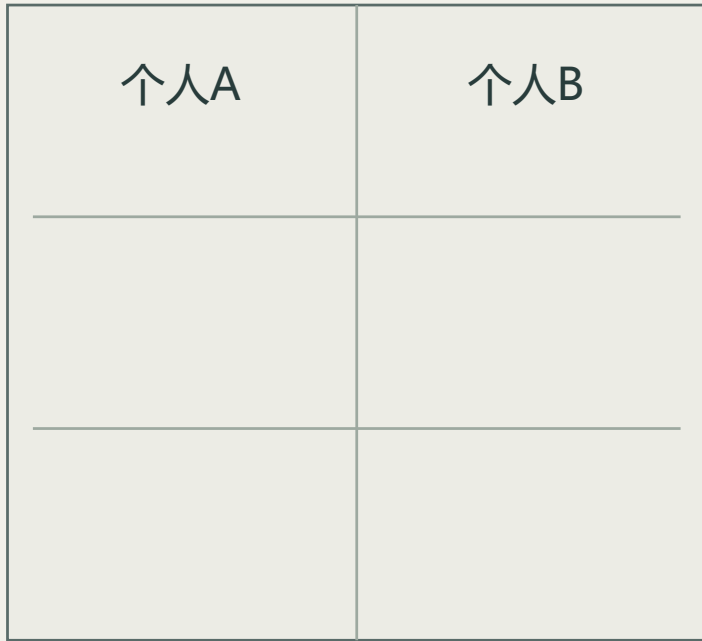

分格意向 / 层板位置按瓶高调整

现有双镜门保留

外550×150×800；门约271×2；层板几何深116。

干湿与电源分开

湿牙杯放可取托盘；充电点须专业确认，不能塞普通插排。

干衣与湿物不是一个仓

门扫掠外试挂干衣、擦身毛巾；污衣可提走，盆下管线可达。

镜柜按人和瓶高分

两扇约271宽镜门已存在，不是本轮新增。层板几何深116，仍需扣门铰、灯线和背构造；牙刷、护肤小瓶分人分格，活动层板随最高常用瓶调整。药品与湿毛巾不默认存潮湿镜柜。

电源与湿物分仓

带电剃须/牙刷充电仅在湿区电气专业允许的位置与构造中设点，不能把普通插排藏进柜即称安全。湿牙杯、接水托盘与电源隔开，取用线不跨洗面活动区。

临时衣物与管线都有位置


干区、门扇包络外预留换洗干衣和擦身毛巾挂位，脏衣用可提篮及时移阳台，不常驻堵路。盆下让出角阀、存水弯及检修，只放可取托盘；淋浴薄架须不碍肘和门，不先凿结构、外墙或管井做壁龛。

依据 | G03 p4-7、17、28、44、53-54、64、84、86、105


阳台与生活阳台平面索引与空间示意

方案设计交付版 · 沿用R3设计条件 · 尺寸单位mm · 待现场复尺及厂家深化

01 / 空间平面与柜号

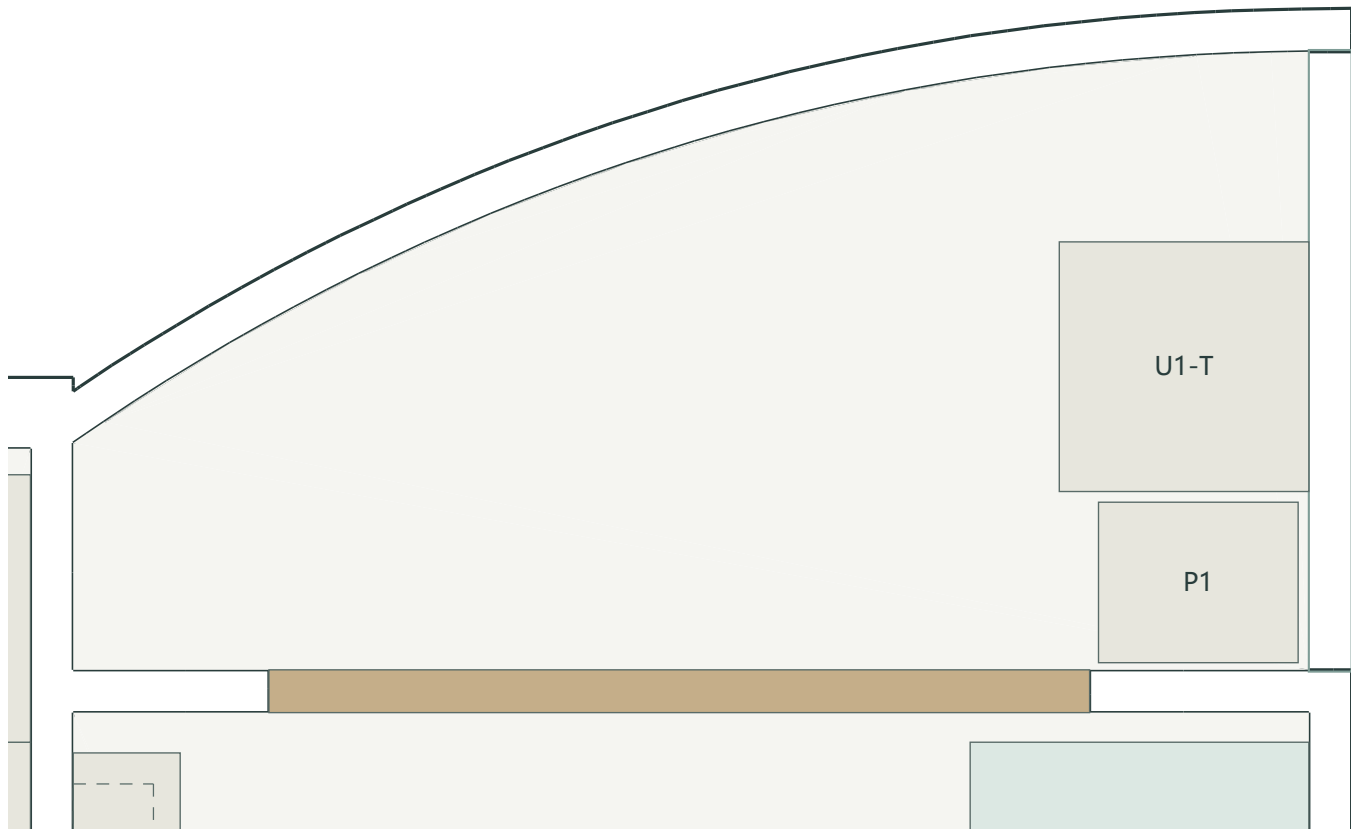

02 / 关闭外观

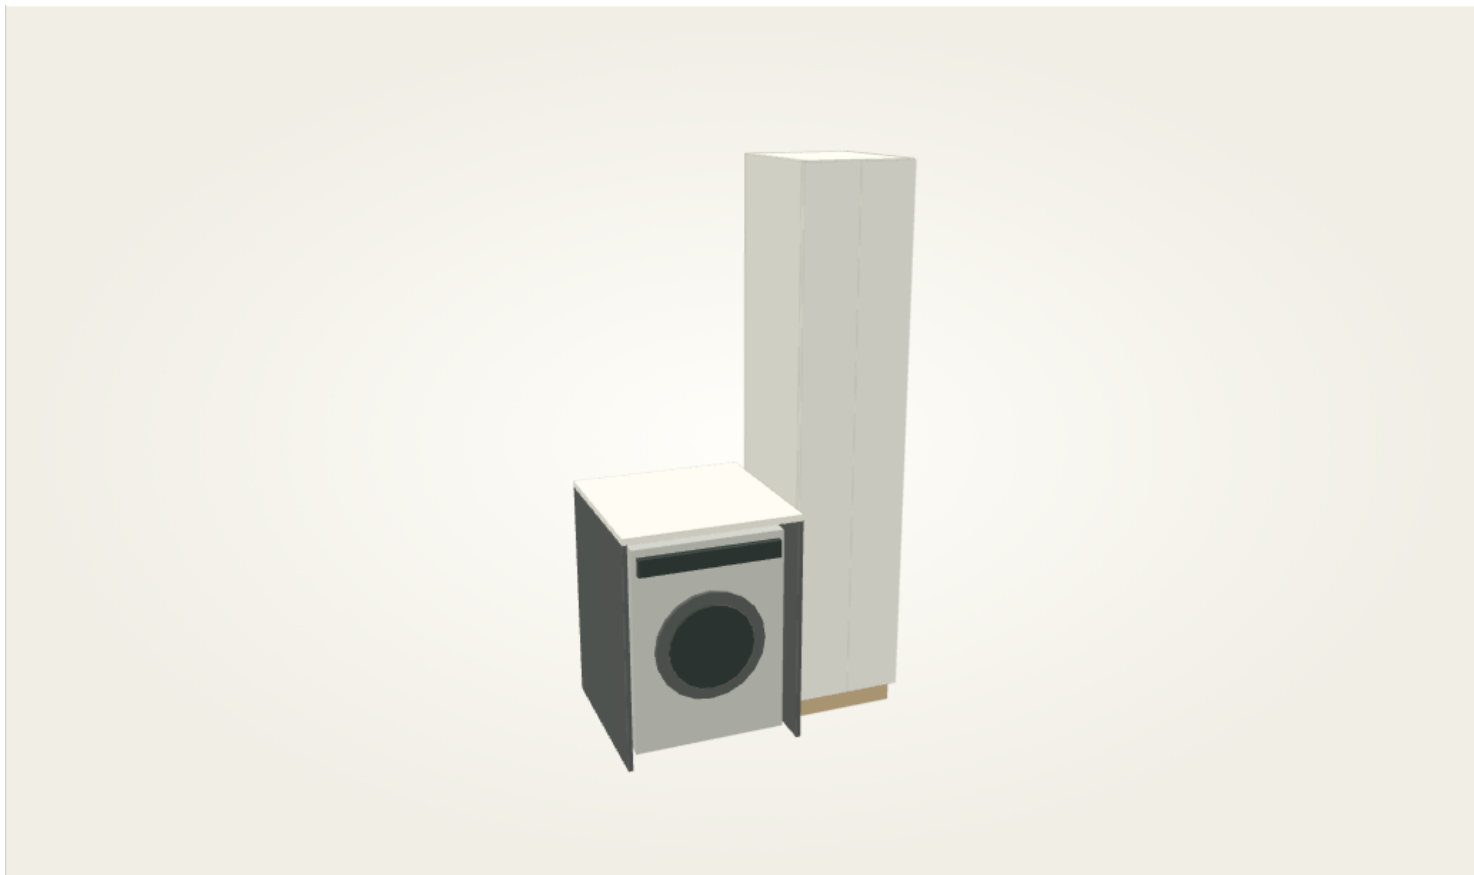

布置与使用要求

主阳台端部洗衣、家政，中央留采光与晾晒；生活阳台U3为低柜，不密闭包裹燃气设备。


读图及现场确认

平面编号与P-03、T-01/T-02对应；正立面按柜体朝向展开。三维图为剖墙示意，不是照片级效果图。尺寸和设备以本册控制值及复尺结果联合确认。


阳台与生活阳台柜体正投影展开

方案设计交付版 · 沿用R3设计条件 · 尺寸单位mm · 待现场复尺及厂家深化


P1 / 正立面

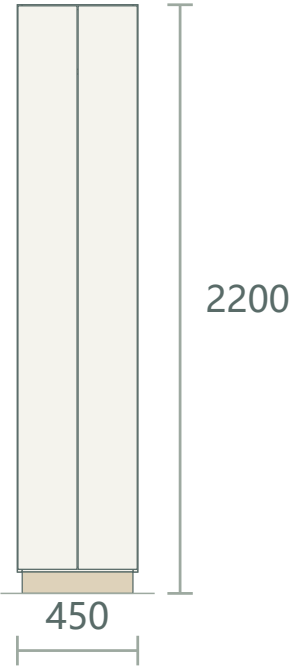


P1 / 去门板内部投影

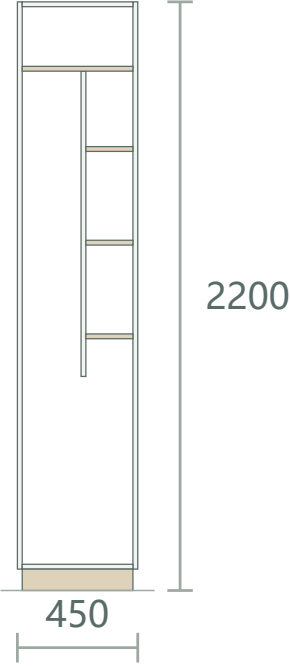


U1-T / 正立面

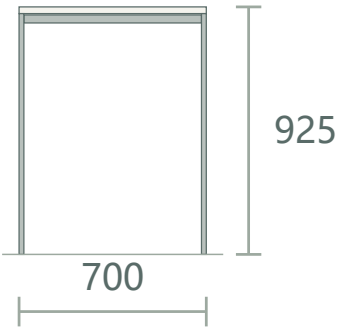


U1-T / 去门板内部投影

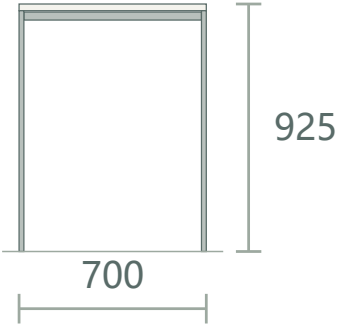

U3 / 正立面

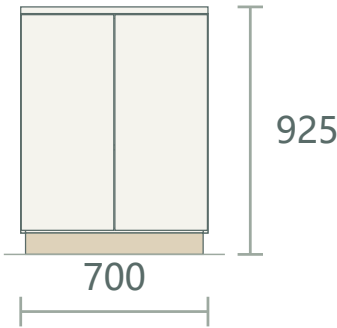

U3 / 去门板内部投影

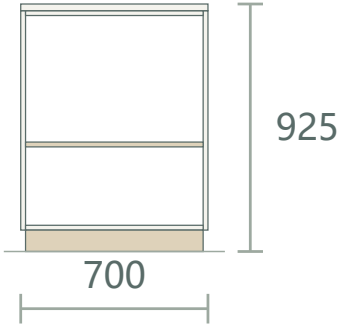

沿模型轴递增展开，非站位左右；标注柜体外包宽高，板厚为模型占位。内部去除门板和背板，非取消构件；不作为板件拆单。

家政柜与洗衣台控制

方案设计交付版 · 沿用R3设计条件 · 尺寸单位mm · 待现场复尺及厂家深化



洗 → 整 → 晾，分时操作

台顶925、台底900；独立支架不压机器。

P1端部家政柜

450×560×2200；底部净414，上部分220与176。

曲边阳台不套矩形案例

不加整墙1500/1800柜；中央采光、抽机转弯与晾衣冲突一并看。

保留可真正抽机的路径

设备候选630×660×870并非任意滚筒都适配；台底900、台顶925由独立框架承托，不压机器。门、洗涤剂抽屉、滤网、阀门、插座及整机抽出转弯一并核，台前不固定篮柜。

家政柜底部保持414宽

大刷头/桶在低区，上部分220与176净宽，隔板800起；先按刷头、机身、长柄与拿取角度定收纳。湿拖布干燥后再关柜；托盘可取，清洁剂与洗衣篮分仓。

不套整面阳台柜

指引1800/1500宽柜、矩形1800×3400阳台示例不适配本案曲边。设备靠端部、中央采光保留；晾衣下降与装卸分时，挂满衣物确实会遮光，脱水噪声也不会因风水偏好消失。

依据 | G05 p5、6、21、23、38、39、43、44

生活阳台低柜与设备维护

方案设计交付版 · 沿用R3设计条件 · 尺寸单位mm · 待现场复尺及厂家深化

上方原设备

热水器、烟道、阀门，不包成密闭家具。

中间可维护空间

检查、关阀、拆件；不算储物容量。

下方U3低柜

700×680×925；几何净664×644，清洁备品可取盒。

防潮板不等于防水；柜体防水也不等于电器可以露天。

备品低柜

放大瓶清洁剂、备用纸品和可取整盒，不作为食品柜。层板可拆，前非常用、后排成盒；厚背板、墙距和管件扣除后再选箱，不能用680外深直接购箱。

热水器与管路不装饰性封死

不照搬指引中隐藏热水器、管线满包或窗前高柜的示例；燃气设备的进排气、排烟、检修与阀门操作始终可达。热水器和灶具安装由合格人员按实际说明书完成。

两阳台环境选材


先核防雨、日晒、温湿与渗漏，再选柜材及五金。防潮板不是防水板，防水柜不等于电器可露天；洗衣废水接入何种系统由现场核，不能仅以有地漏证明可用。

依据 | G05 p19–20、22、28–31、34；G02 p59、74、130；燃气官方安全资料E01

柜体通用构造与厂家深化节点

方案设计交付版 · 沿用R3设计条件 · 尺寸单位mm · 待现场复尺及厂家深化

D1 / 干区层板与背板关系

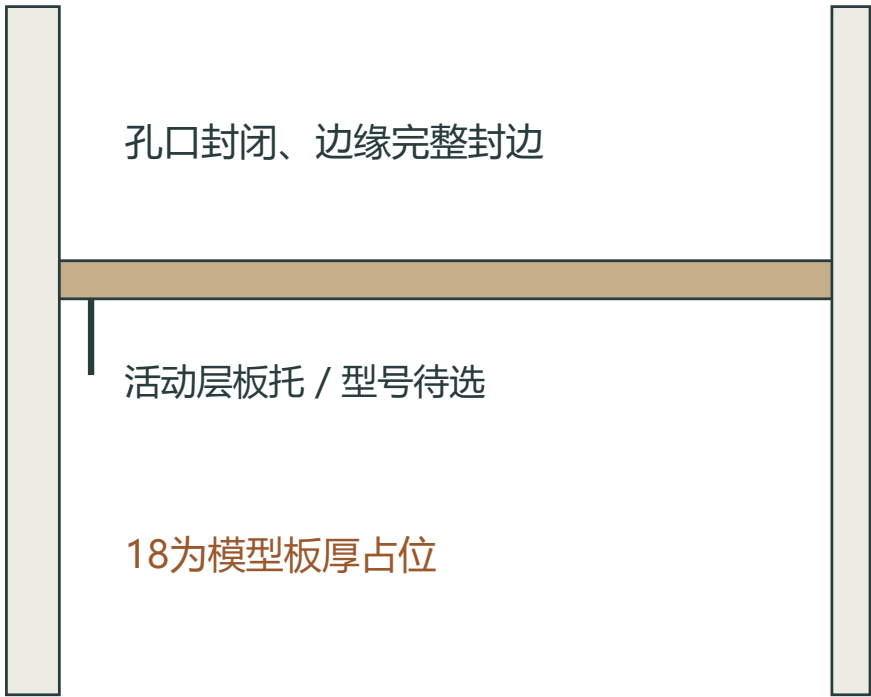

D2 / 洗衣台独立支承原则



机器与台面不接触承重；框架截面待计算。

深化节点	厂家须提交的内容
D3 湿区	盆体与台面独立可靠承托；管孔封口，接水盘可取；存水弯/阀门/净水换芯不被背板封死。
D4 高柜固定	固定点、锚栓、墙体基层及抗倾覆由现场与厂家出详图；禁止按模型随意钻结构墙。
D5 电器邻接	灶、凯度分别满足许可、承托、隔热和连续通风，不给未经选型的隔热板或通风缝生产尺寸。

灯光与设备接口功能要求

方案设计交付版 · 沿用R3设计条件 · 尺寸单位mm · 待现场复尺及厂家深化

照亮动作

备餐照台；镜前照脸；夜灯不直射枕头。

留可维护构造

灯、驱动、开关、插头都能取出维修。

专业落实电气

现场负荷、回路、湿区边界及产品安装要求。

当前仅定义功能和避让，不提供未经现场核验的开槽坐标。

玄关、厨房、餐边

玄关随手台和鞋格有独立补光，感应避免只要开门就全屋亮。厨房吊柜下照备餐台，避免人在中央顶灯前形成阴影；灯槽可擦洗，驱动可更换。餐边电源避机器背部和热蒸汽。

卧室与浴室

两床分侧控制壁灯/阅读灯与充电位，不加常规大床头柜挤通道。梳妆/浴镜均匀照脸；感应夜灯避直射枕位。装灯和充电位置以实际身高、床面、镜面及湿区边界定位，不给未经现场确定的施工孔坐标。

设备清单一起走线

冰箱、洗碗机、蒸烤、独立微波、三台空调、洗衣机、净水、机器人、热水器和电视分别核负荷/接口。插座不占背部安装净深或阻挡抽机；不用同一插排串接多台大功率设备。

依据 | G04 p35、54；G02 p38、69、73；G03 p28、44、49、50、105

柜体与保留家具总表（一）

方案设计交付版 · 沿用R3设计条件 · 尺寸单位mm · 待现场复尺及厂家深化

柜号	对象名称	宽×深×高 / 特殊口径	控制要求
K1	750灶柜与747双槽联合湿区	2247×600×2700	台高860；150+750+600+747；凯度条件位
K2	750×600平嵌冰箱位	750×600×2700	750×600设备控制；设备高1980为占位，不是2700整机
K3	600深微波与可拆锅具柜	620×600×2700	独立微波；下部锅具可拆，保留凯度回退
K4	扫地机器人检修组合	600×600×2700	基站净宽564；上盖开启维护
K5	浅餐边柜	830×350×2700	下台高860；上宽400、深300；其余退让
M2	长衣优先可变衣柜	1050×600×2700	主杆1800；底盒移出；可调1750-1910
M3	梳妆与浅储物组合	750×600×2700	台高750；上柜底2000、深300；镜可关
S2	三模块可调整衣柜	1500×600×2700	双杆1850/940；第三格1850；上段退台
S3	窗下浅柜	700×280×800	内深约224；不作站台
P1	宽底可变家政柜	450×560×2200	底部净414；800以上分220/176

柜体与保留家具总表（二）

方案设计交付版 · 沿用R3设计条件 · 尺寸单位mm · 待现场复尺及厂家深化

柜号	对象名称	宽×深×高 / 特殊口径	控制要求
U1-T	独立整衣台与洗衣位	700×700×925	台底900、台顶925；独立承托
U3	原洗衣位备用低柜	700×680×925	热水器阀门保持独立开放检修
R1	鞋包柜	1200×320×2700	台高1000，上柜底1550；与3D同号
L2	电视低柜	2000×300×450	电视中心1100；机身示例1675×962
L2-U	电视上方浅柜	800×230×500	底2200；保留既有浅柜，不新增满墙柜
M5	主卧门上浅柜	840×300×500	底2200；门位待核，轻物
B2	盆柜	550×400 / 台顶860	柜底220；前凸盆另算
B3	镜柜	550×150×800	底1100；层板几何深116
M1	主卧床	床垫1500×2000	顶470默认/520对照；窗台600仅模型
S1	次卧床	床垫1500×2000	床面520；固定床保留

饰面与基材选型表

方案设计交付版 · 沿用R3设计条件 · 尺寸单位mm · 待现场复尺及厂家深化

编号 / 名称	适用对象	选型及构造要求	确认与验收
MAT-01 干区柜体与门板	干区：R1、L2、L2-U、M2、M3、M5、S2、S3、K2至K5；电器邻接另核MAT-03	18毫米板件方案占位；暖白平板门、浅木纹局部；完整封边，开孔处封闭处理；索取对应产品检测资料	样板、板材品牌与基材待选
MAT-02 厨房/潮湿低柜	K1湿区/B2盆柜/K4底部/U3；B3镜柜按湿区环境选材	优先比较金属湿区柜体与可靠防潮板方案；可取出接水托盘，管孔封口，底部不直接吸水	询价时分项列明构造
MAT-03 电器承托与邻接表面	K1凯度条件位 / K3独立微波及回退	按两台设备说明书选择承托、间隙与耐热构造；插座和检修口位置可达	机型确定后由厂家与电气专业复核
MAT-04 阳台柜体与五金	P1/U1-T/U3按实际环境	环境确认后选适用的耐候金属柜体/饰面及防腐五金；若完全室内化可另比较干区方案	现场雨晒条件优先
MAT-05 台面	K1/K5/U1-T/U3	厨房860高与阳台925高按原控制线；台面材质、接缝、开孔支撑与滴水边由厂家详化	实体样板和施工节点待选

五金配置与验收表

方案设计交付版 · 沿用R3设计条件 · 尺寸单位mm · 待现场复尺及厂家深化

编号 / 名称	适用对象	选型及构造要求	确认与验收
HW-01 抽屉滑轨	K5浅抽/S2抽屉/M3薄抽； K1现为灶下条件机位，不计 锅具抽屉	标准可替换型号；缓冲；长度、净空和额定荷载按具体宽深与物品核定	不按品牌名称默认所有规格承重相同
HW-02 平开/移门五金	各柜普通门及S2浅顶柜	按门重、门高和开启角度选型；门铰与内抽屉无干涉，限位可调	未完成门重及安装图前不指定铰链数量
HW-03 主卧双折门系统	M2	保留四片联动构型；防夹、限位、承载和双侧折叠停车位由供应商实体 样验证	动画示意不等于五金认证
HW-04 机器人台盖支撑	K4	按盖板自重与操作选择限位、支撑及防夹结构；维护时不放重物	不把活动盖当常驻电器台
HW-05 活动层板与挂杆	M2/S2/S3/P1/U3	侧板排孔/可拆支座；层板跨度、荷载及挂杆挠度厂家核验	示意满格不是满载试验
HW-06 洗衣台独立框架	U1-T	台面独立承托，机器落地调平；支脚不侵占设备候选安装位	不压机器、不用未获允许的软垫/轮架

电器及设备条件表（一）

方案设计交付版 · 沿用R3设计条件 · 尺寸单位mm · 待现场复尺及厂家深化

设备	位置	占位及口径	下单条件
E01 米家套装天然气灶	K1	750×600×860 本轮灶柜750外宽，研究开孔670×360；两者都不是所选灶具机身尺寸或最终模板	精确型号/气源、面板与底壳尺寸、台面开孔和支撑、窗墙距、阀门/燃气管/通风；下方凯度微蒸烤须双方安装许可及节点通过
E02 米家净烟机3 Pro	K1	未锁定 按用户适配图900柜间预留、895图示宽、机体图示上沿高差690-760重建；不是最终厂家CAD	精确外形与预留宽深、烟机和灶面距离、侧翼/油杯拆取、挂板、烟管/止回、进出风及相邻吊柜/窗边界；不得套用旧Pro/P2或3Max安装图
E03 洗碗机	K1	600×待核×待核 600净开口类别，其余安装要求待厂图	机身/装饰门/踢脚联动、碗篮拉出、进排水与可达电源
E04 净水器	K1-W 联合湿区右下	200×450×450 候选机体占位，不含接管与换芯	完整200×450×450机体保留；无固定中隔，前抽600示意。必须核对接头、换芯方向、双槽下水组件、铰链与维护路径。
E05 平嵌冰箱	K2	750×600×1980 宽750、深600为本轮用户指定控制体量；高1980暂沿旧占位，不等安装认证	750净宽内不额外扣侧板；安装缝、散热、门铰/内抽取出、搬入及电源可达按所选机型；邻服务柜本轮同改600深；平嵌仍须各自机型许可
E06 凯度微蒸烤条件机位	K1灶下（条件）；K3为回退	595×555×455 GR Pro只作尺寸参考，尚未决定采购型号。机底标高180、机顶635为本轮研究位。	米家灶与凯度双方允许上下组合；核灶底100接管净空、独立通风路径、承托/电源检修和低位热盘动作。若不获许可返回K3。
E07 独立微波炉	K3	584×待核×380 584宽、1190至1570标高为示意机位	独立于蒸烤箱；台式/嵌入式安装许可、通风和开门方向

电器及设备条件表（二）

方案设计交付版 · 沿用R3设计条件 · 尺寸单位mm · 待现场复尺及厂家深化

设备	位置	占位及口径	下单条件
E08 扫地机器人与基站	K4	未锁定 组合柜外包600×600，净宽564，非基站尺寸	进出/回充、取水箱尘袋、清洗盘、顶盖开角，不默认自动上下水
E09 滚筒洗衣机	U1-T	630×660×870 候选安装体量，非最终机身或安装净孔	侧后间隙、管接头、开门、抽屉、底滤网、抽机、防雨防晒及污废水
E10 燃气热水器	U3邻近独立设备区	450×235×640 原模型机体占位	原位阀门、进排气、专用烟道、检修；不得封入普通密闭柜
E11 主卧壁挂空调	M2 / M3避让	840×225×310 机体示意，不含安装检修间隙	滤网抽取、送风、冷凝水/冷媒路由；不因顶柜封堵
E12 次卧壁挂空调	S2避让	820×220×310 机体示意，参考前维护750	下侧墙位置保留；1020宽上柜仅250深，退台不能填平
E13 客厅壁挂空调	本轮柜体不占用	830×225×310 保留原位置	与电视浅上柜分开、冷凝水和检修按机型
E14 台面小电器补核	位置未定	未锁定 待用户核对此前清单，不预设数量或购买	电饭煲/水壶/咖啡机等仅为核对例，未确认前不占据备餐台或机器人检修台

风水要求落实与待核事项

方案设计交付版 · 沿用R3设计条件 · 尺寸单位mm · 待现场复尺及厂家深化

编号	保留的居住与风水要求
F01	两卧1500×2000固定床与图下实体床头保留；无深重吊柜压枕。
F02	主卧飘窗硬质完成面高于床垫顶面，不拿靠背或枕头替代比较。
F03	梳妆镜可关闭，浴室镜朝内，不新增正对床、门或邻楼的反射镜。
F04	入户直段不增柜、不加横屏风；入口高设备退入厅内。
F05	严格遮住入户到阳台视线时，利用既有阳台门内侧可闭的透光不透视遮蔽；打开时仍可见景，不声称永久化解。
F06	沙发实墙背靠，主路线不从沙发背后穿过。
F07	原厨房灶背实墙、灶盆间备餐、厨房可关且保必要通风；不把宅朝向等于灶所在宫位。
F08	主阳台端部洗衣、中央留光；机门、排水去向与传统灶口不混用。
F09	浅洗手盆与原排污优先，不为吉向挤门、长距离移排污。
F10	厕门隔视、排风补风、干湿分区；二维门位与模型有冲突，门对门判断须现场确认。
F11	次卧空调在靠厨房方向墙，保留检修退台，避免枕位直吹。
F12	不设置强制风水摆件，不用颜色、设备或物件抵消真实方位取舍。

沿用原私人报告的八宅口径，东南床头对双方的传统分类并不同时为吉；因实体背靠和使用关系保留，不宣称双方全吉。风水作为文化与居住偏好，不预测财运、健康或感情。

复尺、选型及生产前确认清单

方案设计交付版 · 沿用R3设计条件 · 尺寸单位mm · 待现场复尺及厂家深化

确认项	所需动作	责任方 / 时间
P01 20楼完成面和门位	量墙长、梁底、门洞、门套、开向、窗执手和主卧窗台硬质顶；对齐二维图与模型差异。	量房设计师 生产前
P02 米家烟灶精确型号	补铭牌/官方安装书；已给两张尺寸截图继续采用，不重复要求同图。	用户与设备商 燃气与柜孔前
P03 凯度灶下双向许可	确认双方允许叠放及连续通风、接管、承托；不允许则转K3重新深化。	米家/凯度/定制商 K1生产前
P04 双槽和净水	实物核锅、盆夹、完整下水、阀门和换芯抽出；不加垃圾处理器或柜内垃圾桶。	设备商与定制商 台面开孔前
P05 身高和衣物	试470/520起坐与1800/1850挂杆，记录最高鞋靴/最长衣/工具刷头；据此调活动件。	两位使用者与定制商 内部下单前
P06 卫浴1:1样板	核门位、盆形龙头、防溅、淋浴实净口、马桶管位和窗凹位防水，不让镜门碰头。	卫浴设计及施工方 水电防水前
P07 阳台环境与接口	核防雨防晒、废水接入、防臭防漏、窗防护、柜固定与洗衣抽机路径。	物业与现场专业方 洗衣安装前
P08 电气及弱电	核入户容量、各设备负荷/回路、湿区电源、箱体检修和灯具驱动，不以示意插座施工。	电气专业人员 水电开槽前
P09 隐私界面	实试阳台透光不透视遮蔽的昼夜效果、帘轨门扇关系，接受关闭遮景。	用户与窗帘商 软装确认前
P10 柜门与通道	599、440、402保留为窄点；用实际折门、把手、抽屉和人体试用，不靠模型1毫米余量判断。	定制商与用户 生产前

设计依据与版本说明

方案设计交付版 · 沿用R3设计条件 · 尺寸单位mm · 待现场复尺及厂家深化

编号	设计资料	页数	引用口径
G01	客餐厅精细化设计指引	19页	用户提供；按PDF物理页引用
G02	厨房精细化设计指引	166页	用户提供；按PDF物理页引用
G03	卫浴精细化设计指引	105页	用户提供；按PDF物理页引用
G04	玄关精细化设计指引	119页	用户提供；按PDF物理页引用
G05	阳台精细化设计指引	44页	用户提供；按PDF物理页引用
G06	卧室精细化设计指引	144页	用户提供；按PDF物理页引用

其他设计输入

R3场景及柜体模型；用户提供的米家烟机、燃气灶安装图；凯度候选机型资料；用户确认的风水要求。私人出生资料不纳入本册。

页码均为PDF从封面起的物理页。指引是多个案例/产品体系的汇编；案例尺寸、营销容量、旧设备资料不当作现行规范。采用分类、人体尺度、可调分格、湿干分离和维护方法，不照搬大户型或改结构的示例。

分空间细部页保留来源编号；设计指引中的案例不是本案实测或施工许可。

修订记录与交付范围

方案设计交付版 · 沿用R3设计条件 · 尺寸单位mm · 待现场复尺及厂家深化

版本	内容	使用规则
R1/R2	历史布置、设备及床窗高度研究	保留存档；不得混用旧挂杆与旧电视尺寸
R3	六册指引修订；主杆1800、双杆1850/940、75英寸示例	当前3D设计基线；网页版已发布
R4 / 本册	重编交付顺序；新增目录、平面、索引、正投影、图签和表单	文档交付版；不擅改R3已确认的布局和几何
下一阶段	现场复尺、机型锁定、材料样板、五金及接口详图	责任方确认后再转生产与施工

交付内容与未交付内容

本册交付：可索引的A3方案图册，分空间平面、模型正投影及控制示意、材料五金设备表、风水约束与复尺清单。

未交付：现场签认测绘、结构/机电施工图、厂家板件拆单及正式审图签章。请勿把R4版本号理解为“已批准施工”。